



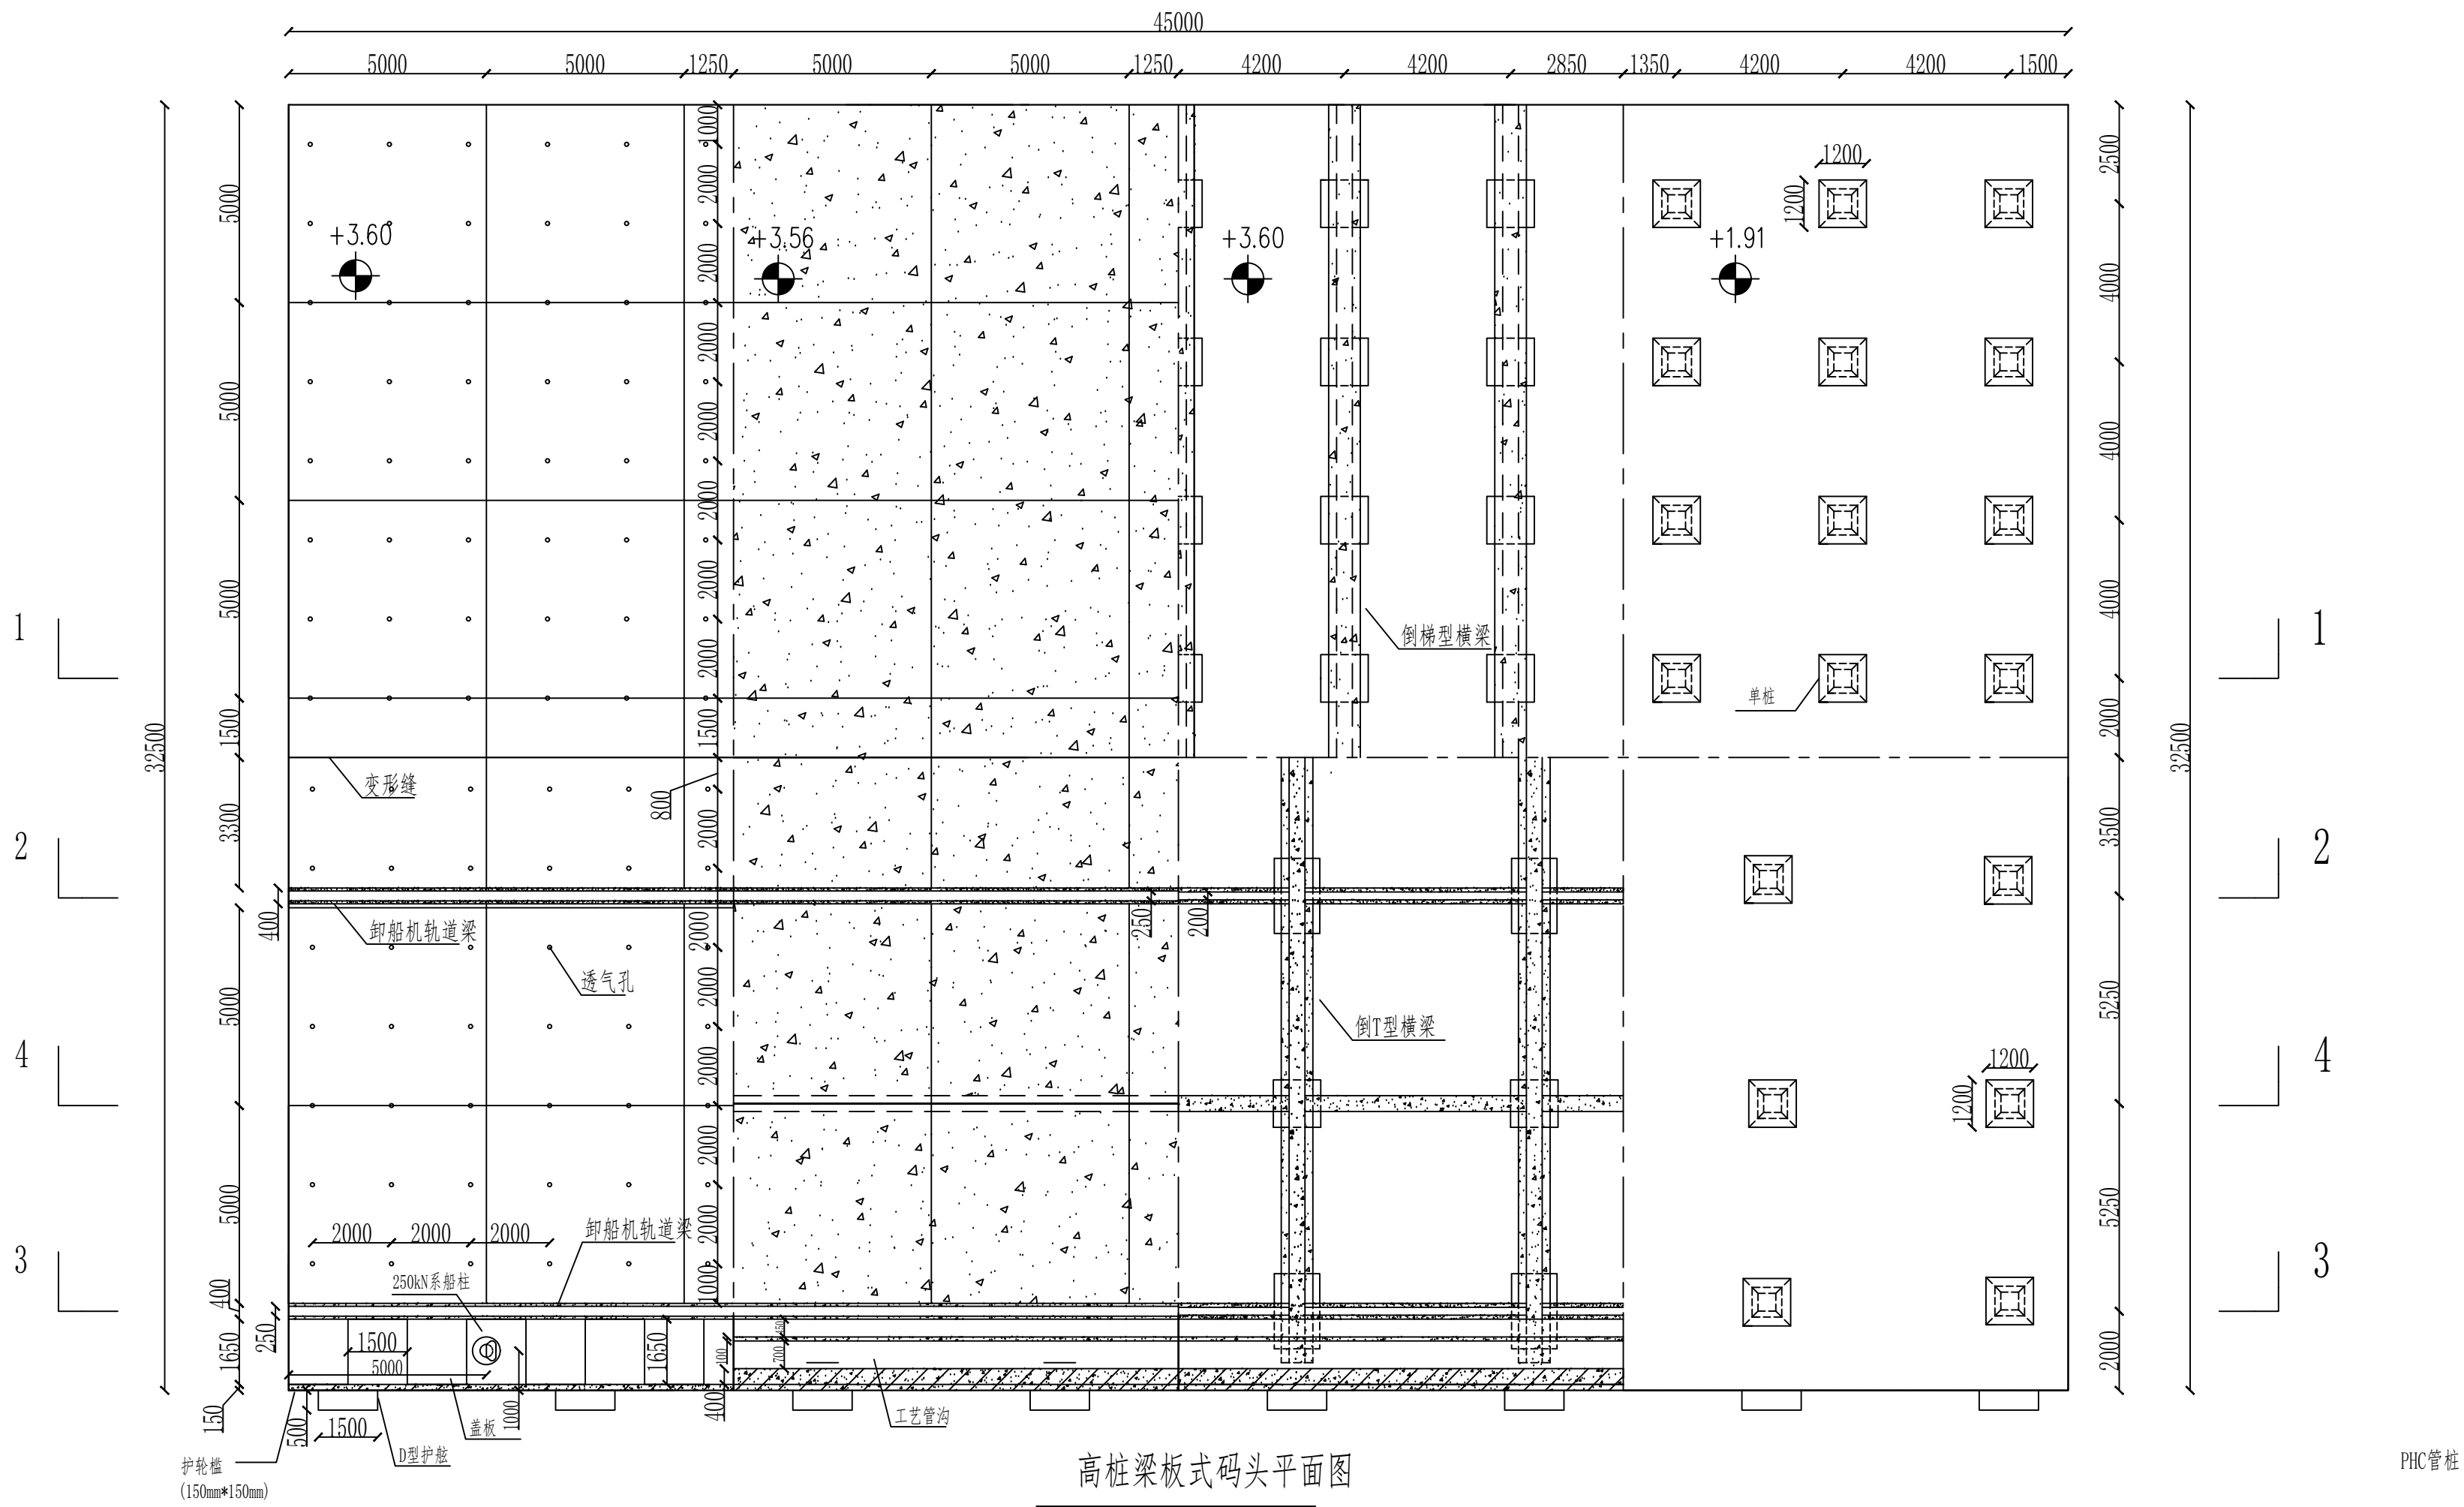

高桩梁板式码头平面图

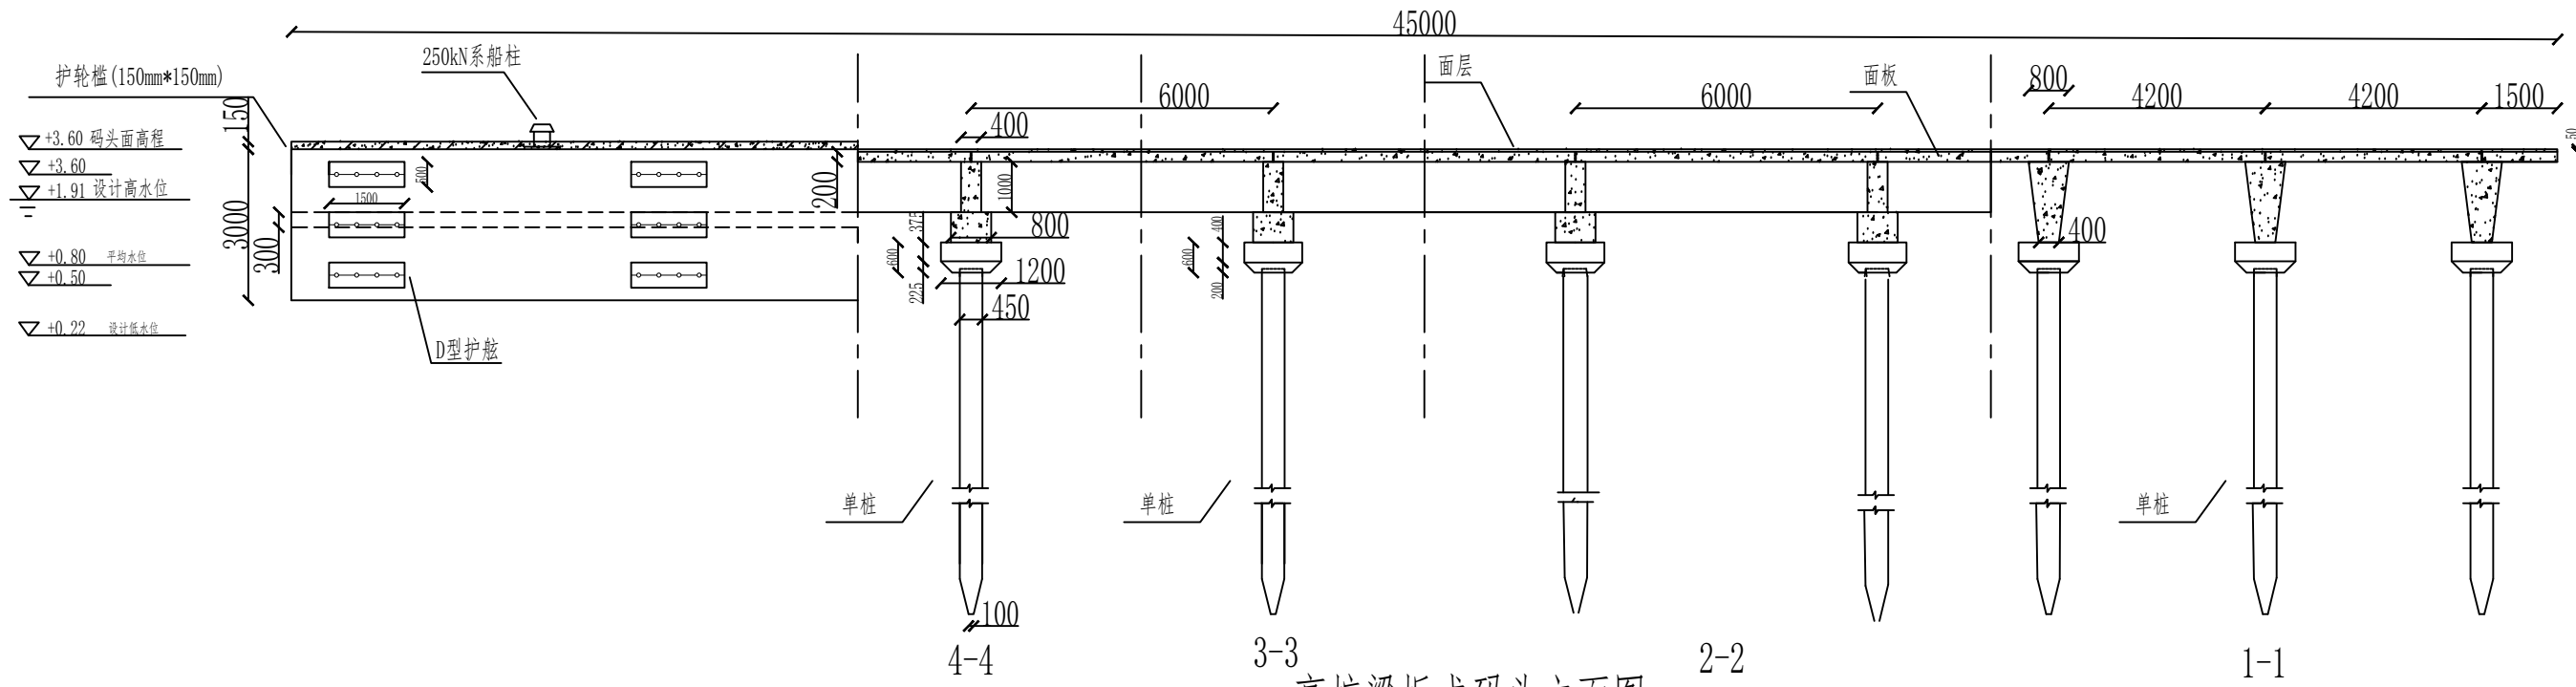

高桩梁板式码头立面图

天津大学		建筑工程学院	
工程名称		港口航道与海岸工程	
图纸内容		指导教师 孙克刚	
姓名 潘欣		学号 3022001703	
班级 2023级港口与航道工程		日期 2026.06	
比例尺 见图示		图纸编号 2/6	