


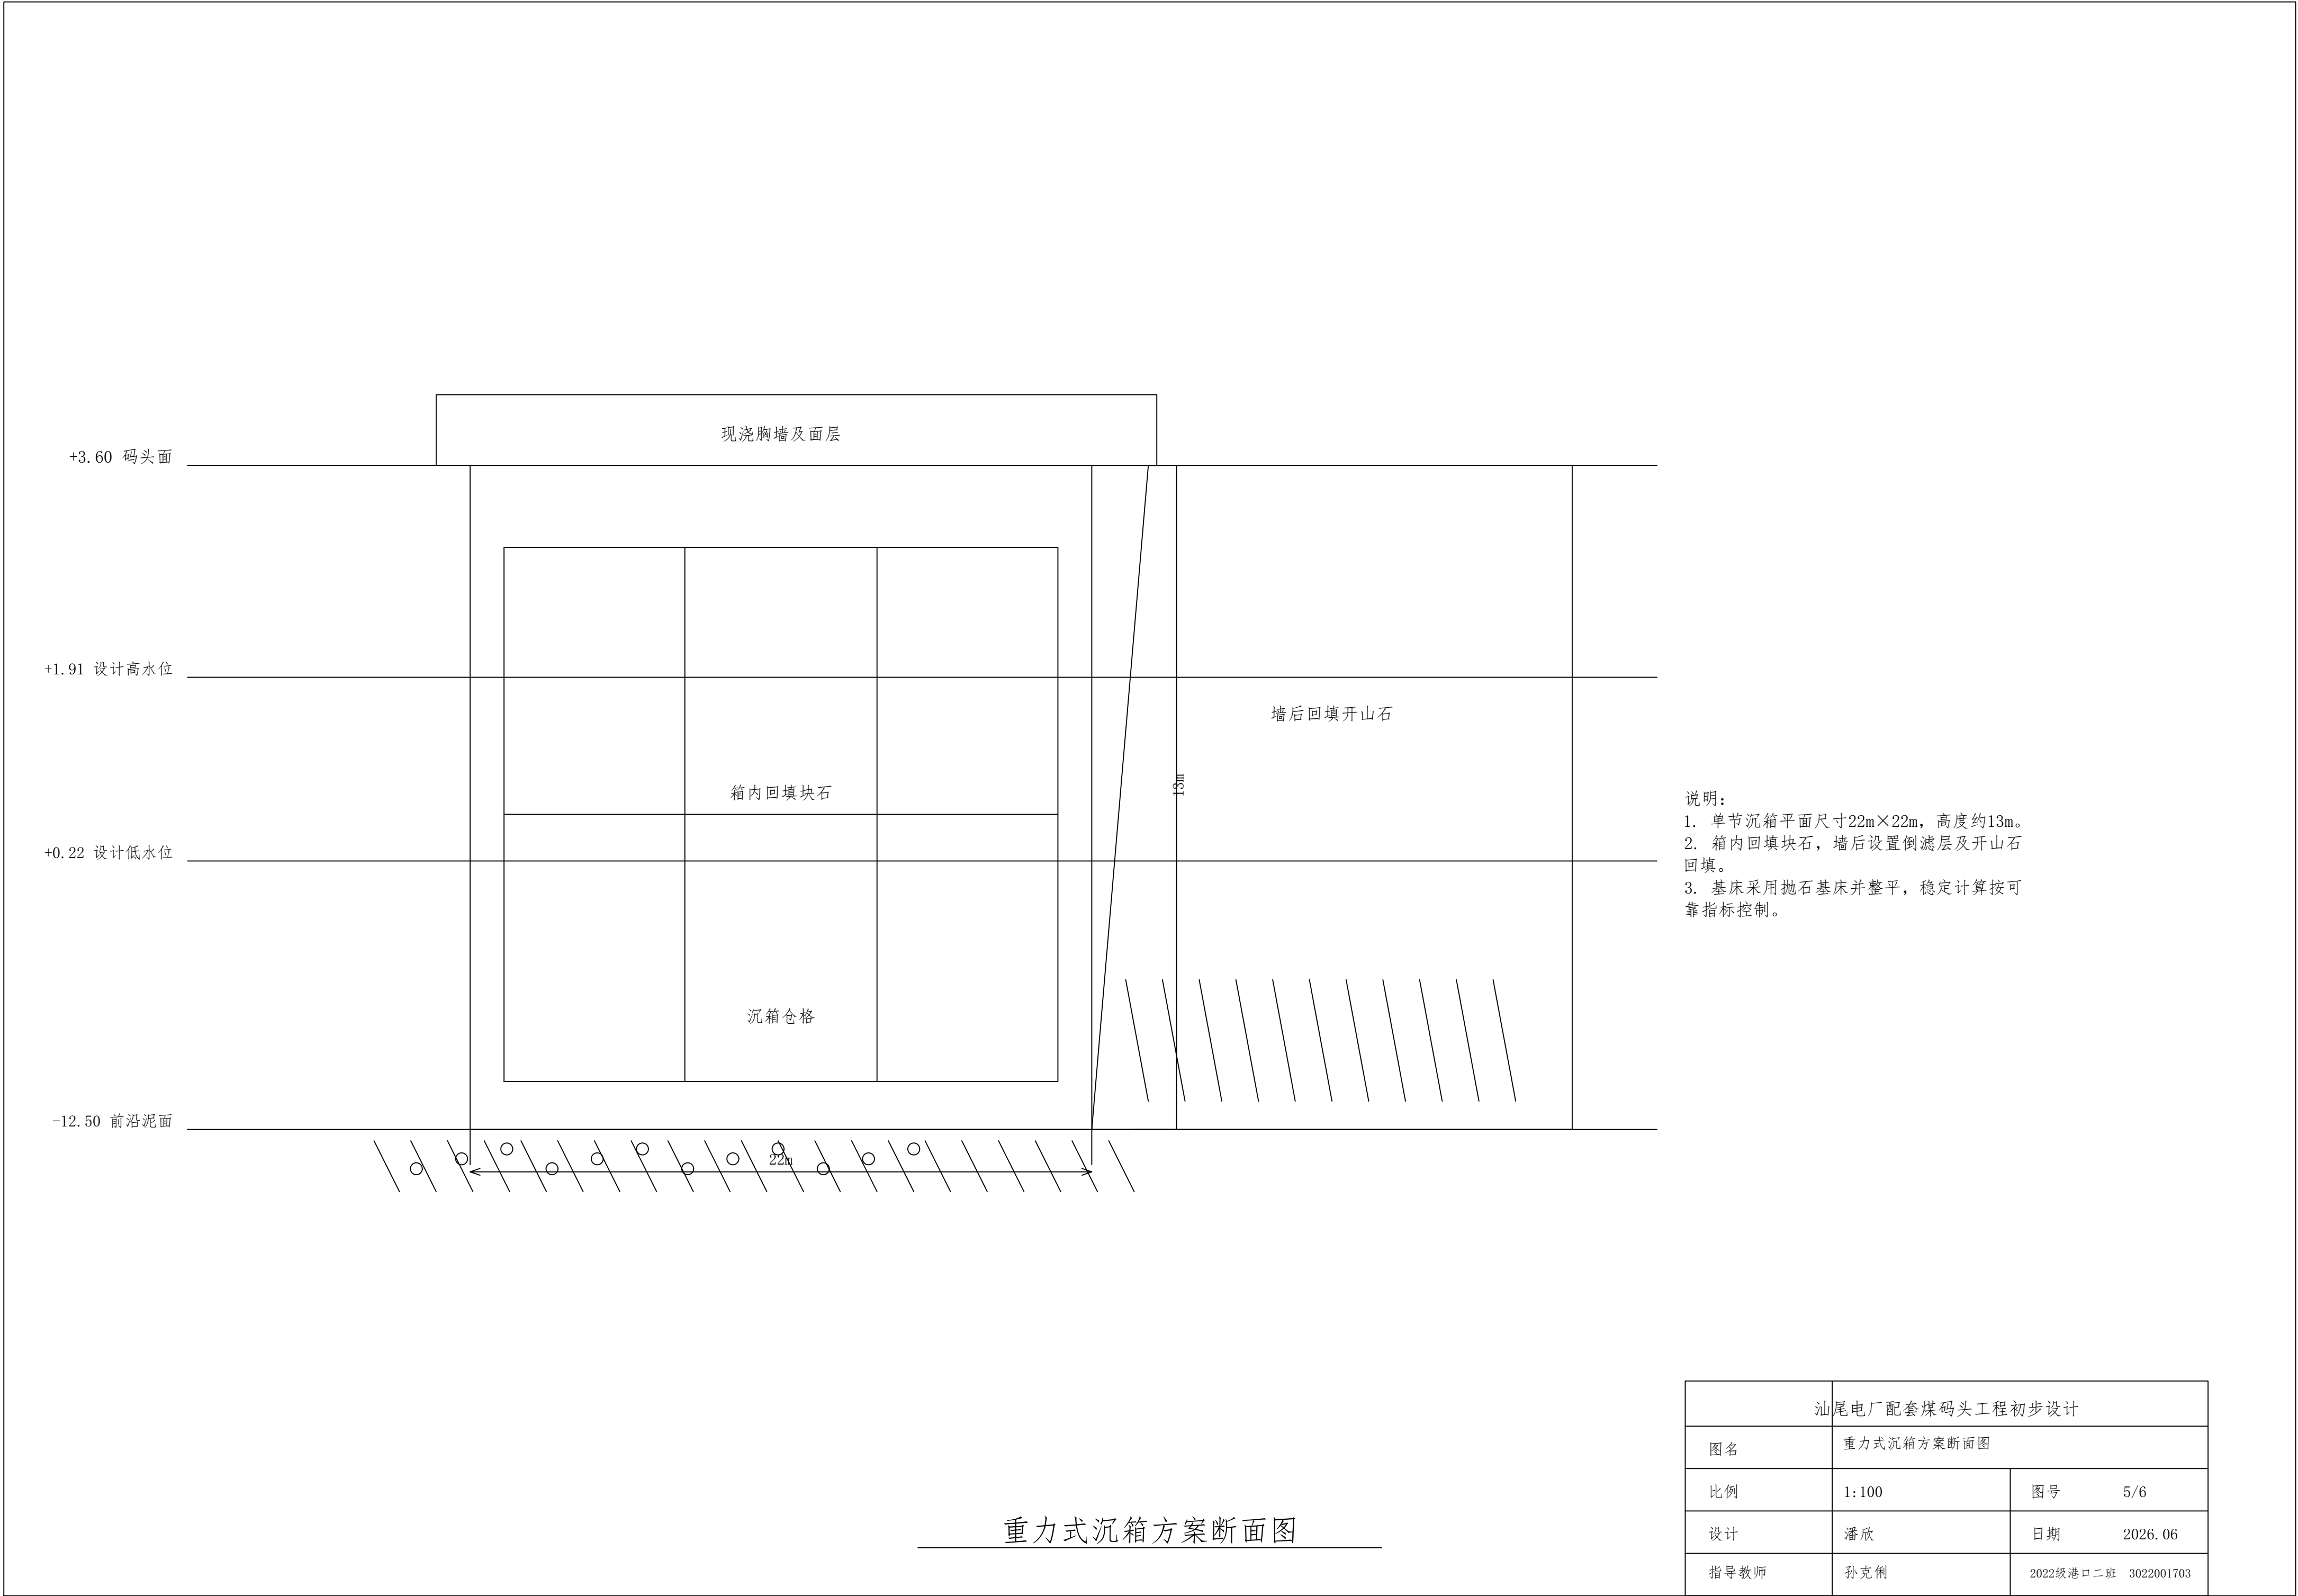

汕尾电厂配套煤码头工程初步设计			
图名	重力式沉箱方案断面图		
比例	1:100	图号	5/6
设计	潘欣	日期	2026.06
指导教师	孙克俐	2022级港口二班	3022001703