
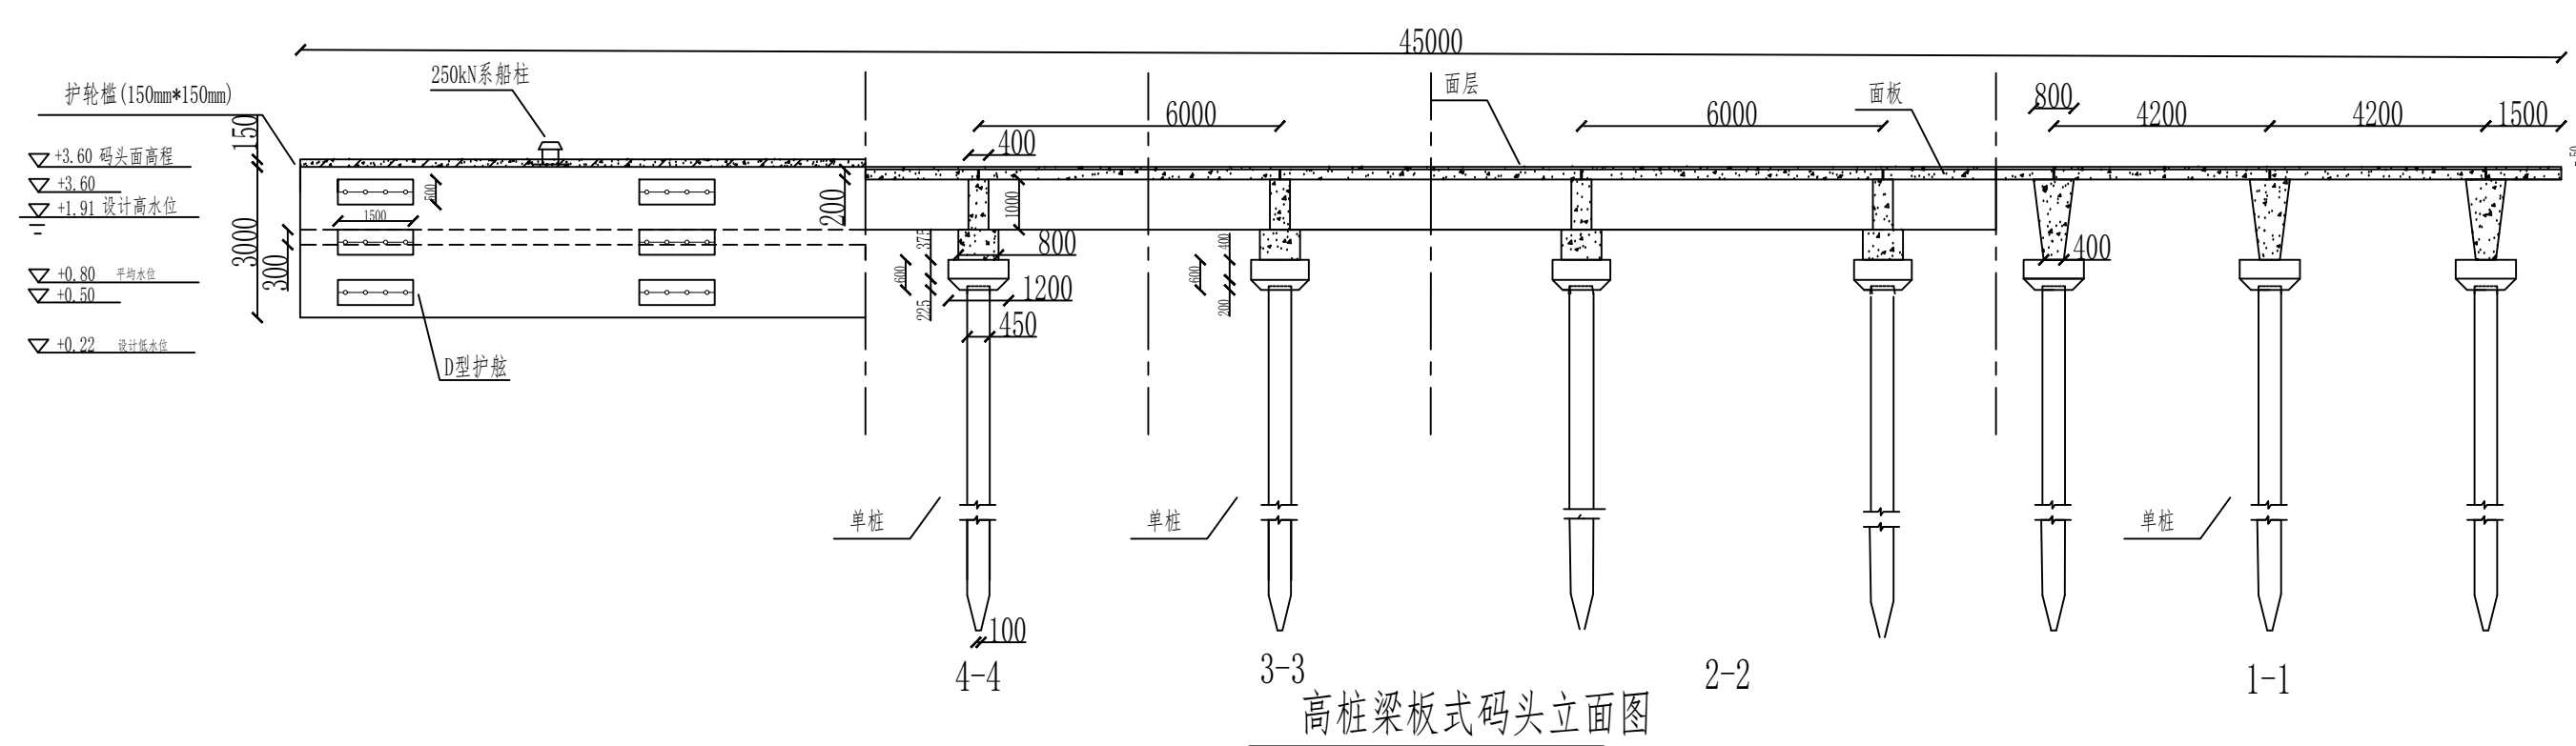


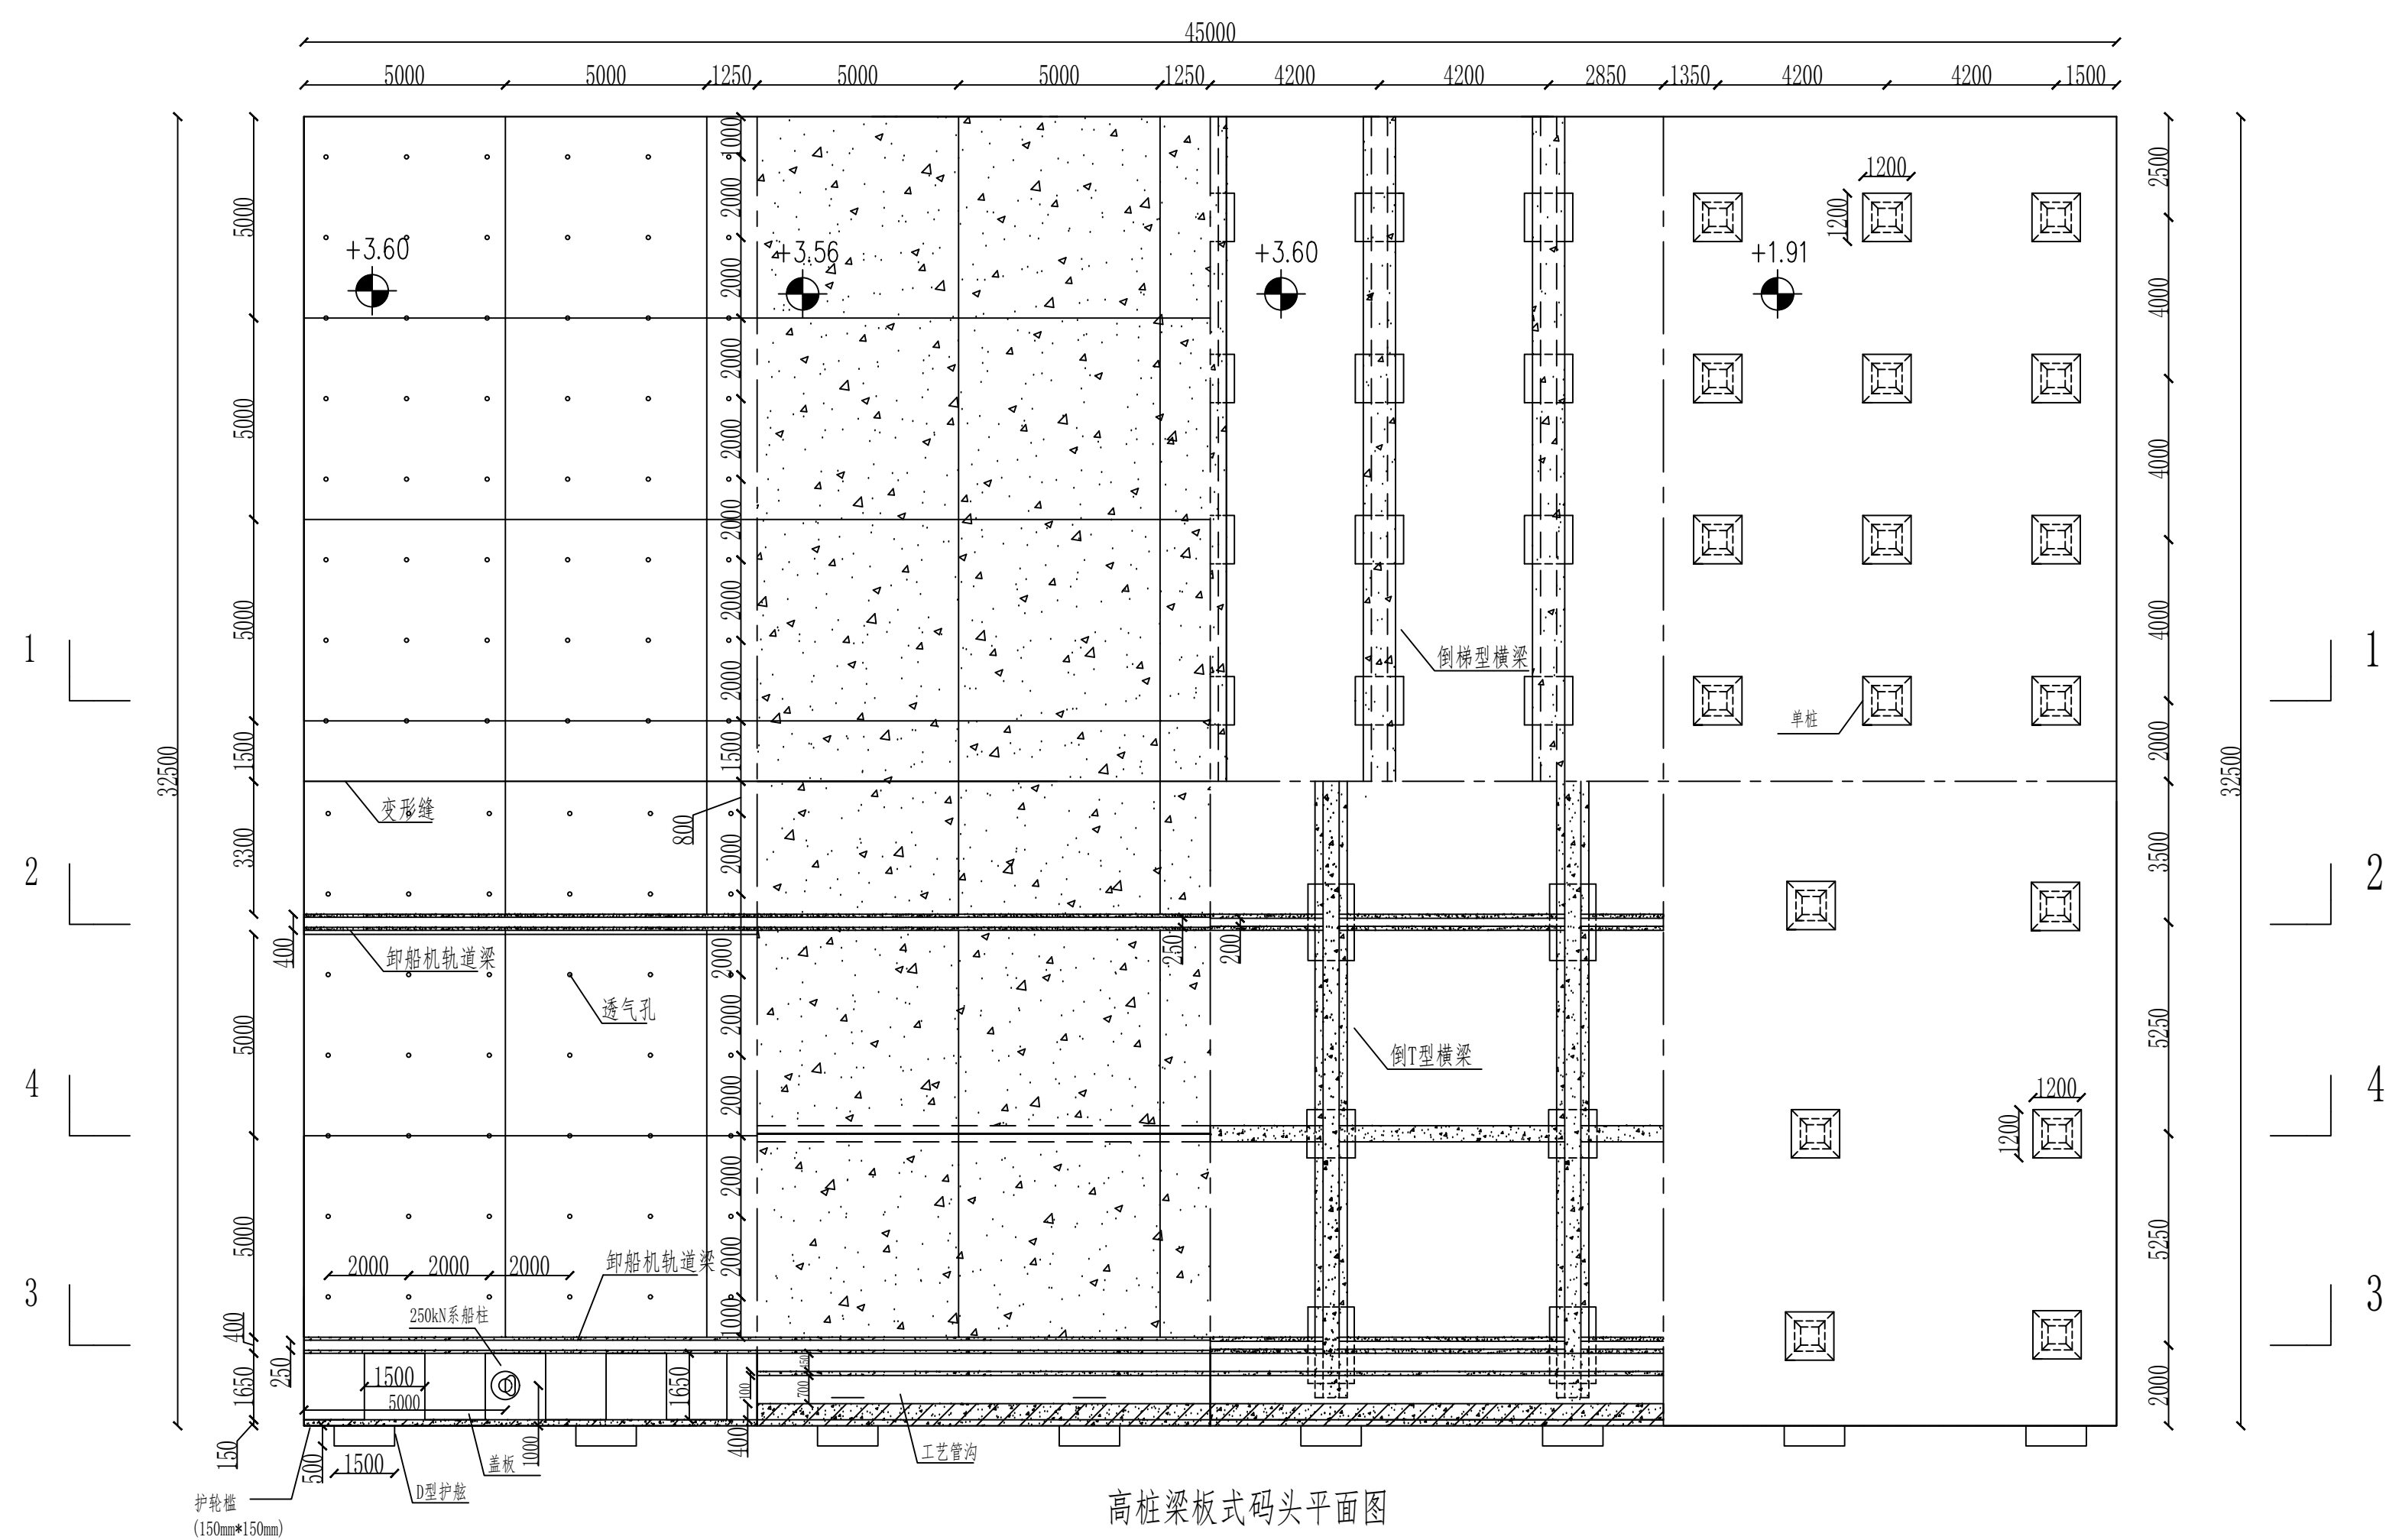

天津大学		建筑工程学院 港口航道与海岸工程		
工程名称	汕尾电厂配套煤码头工程初步设计		指导教师	孙克刚
图纸内容	高程断面式码头 平面图、总图	比例尺	见图示	图纸编号
姓名	潘欣	班级	2022级港口与航道工程二班	学号
			3022001703	日期
				2026. 06