


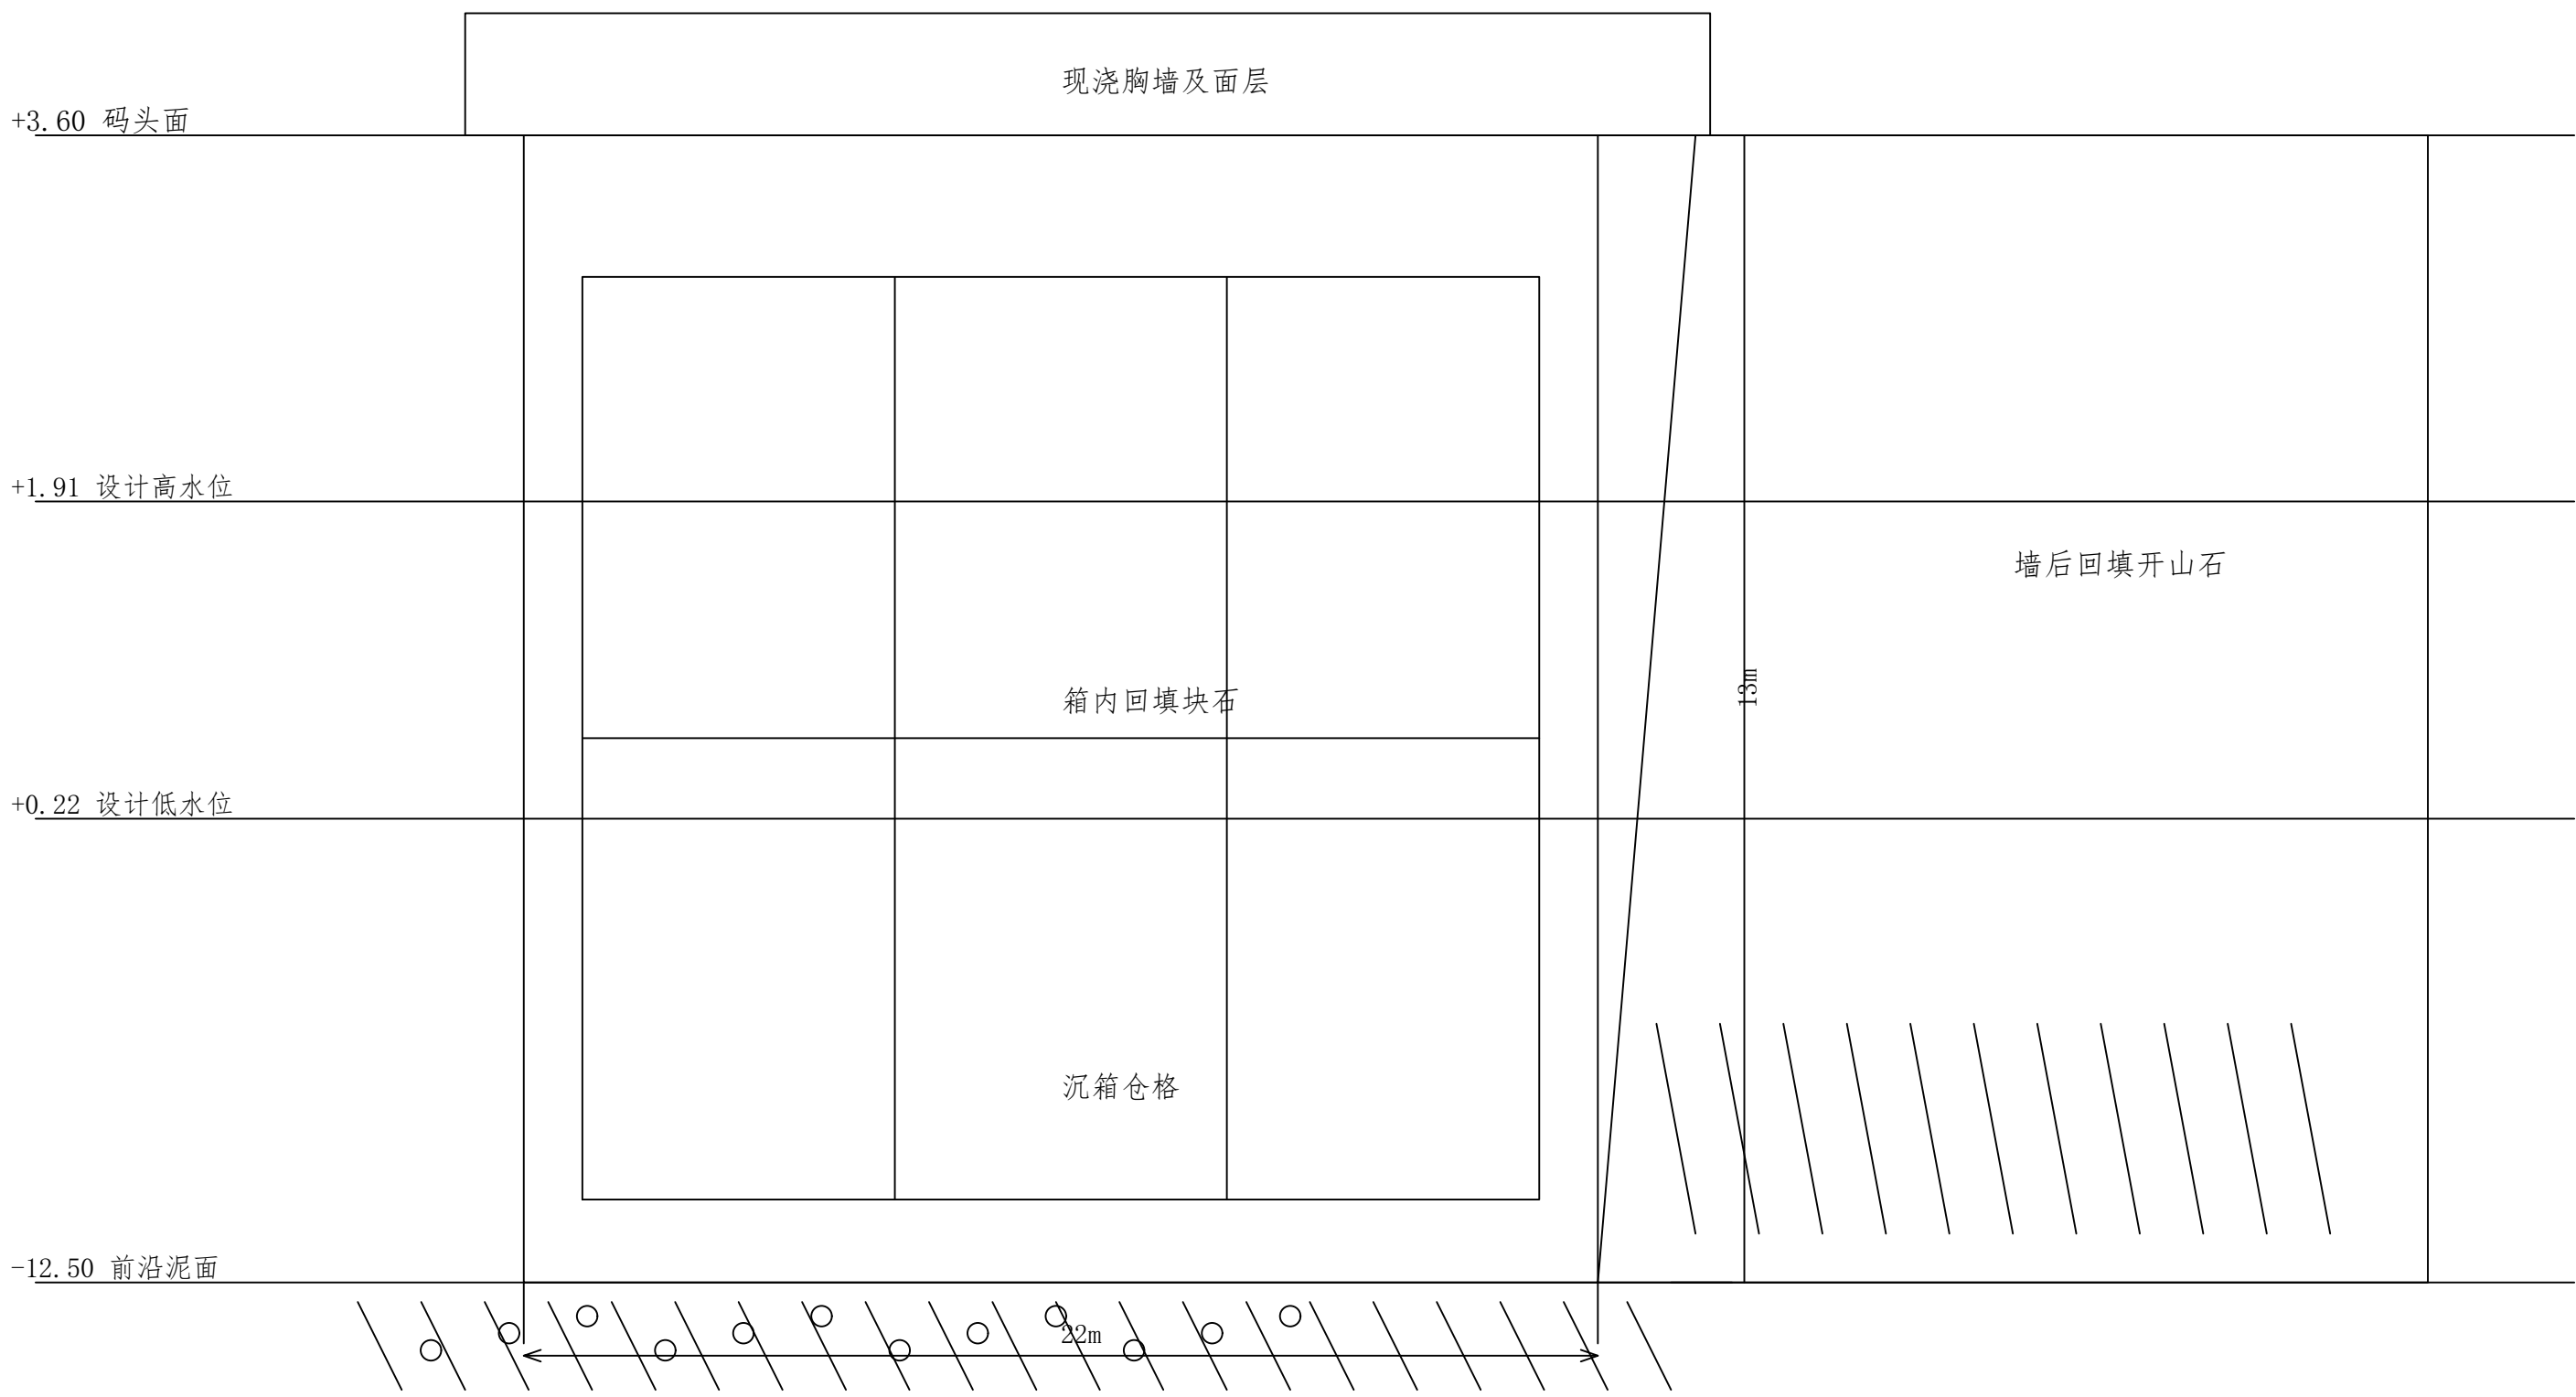

说明：
1. 单节沉箱平面尺寸22m×22m，高度约13m。
2. 箱内回填块石，墙后设置倒滤层及开山石回填。
3. 基床采用抛石基床并整平，稳定计算按可靠指标控制。

重力式沉箱方案断面图

	汕尾电厂配套煤码头工程初步设计	
图名	重力式沉箱方案断面图	
比例	1:100	图号 5/6
设计	潘欣	日期 2026.06
指导教师	孙克俐	2022级港口二班 3022001703