
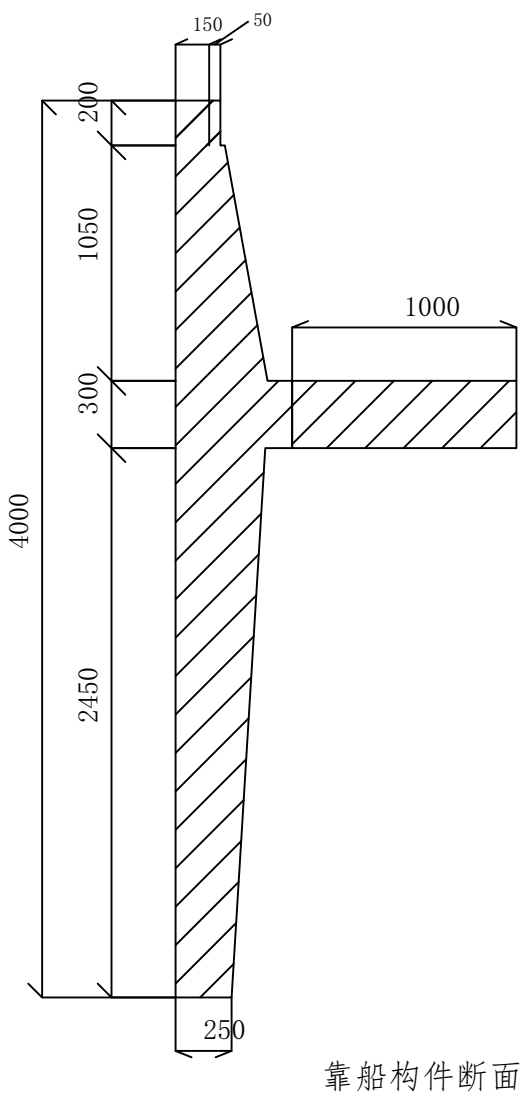
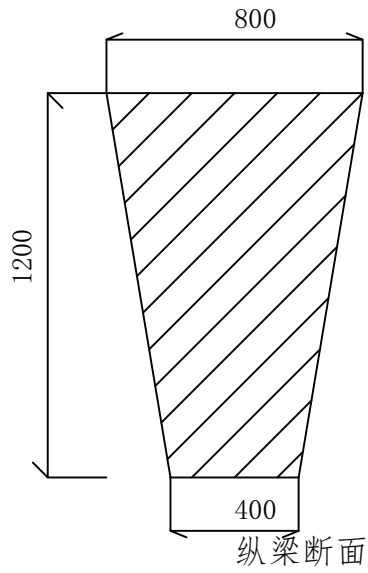


横梁、纵梁及靠船构件断面图（单位：mm）

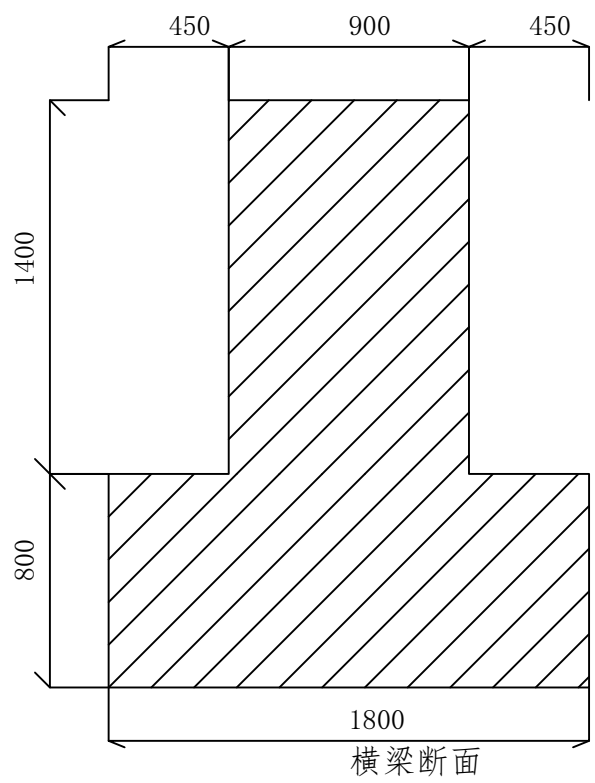

说明：
1. 本图按典型构件断面绘制，尺寸单位为mm。
2. 横梁按1800×2200控制，底部加宽段与桩帽、节点钢筋连接。
3. 纵梁按800×1200控制，底宽400，梁端钢置和湿接缝长度另按构造处理。
4. 靠船构件按前沿局部受力构件绘制，护舷、系船柱连接区应按构造加强。

典型构件尺寸图

	汕尾电厂配套煤码头工程初步设计	
图名	典型构件尺寸图	
比例	1:50	图号 6/6
设计	潘欣	日期 2026.06
指导教师	孙克俐	2022级港口二班 3022001703