
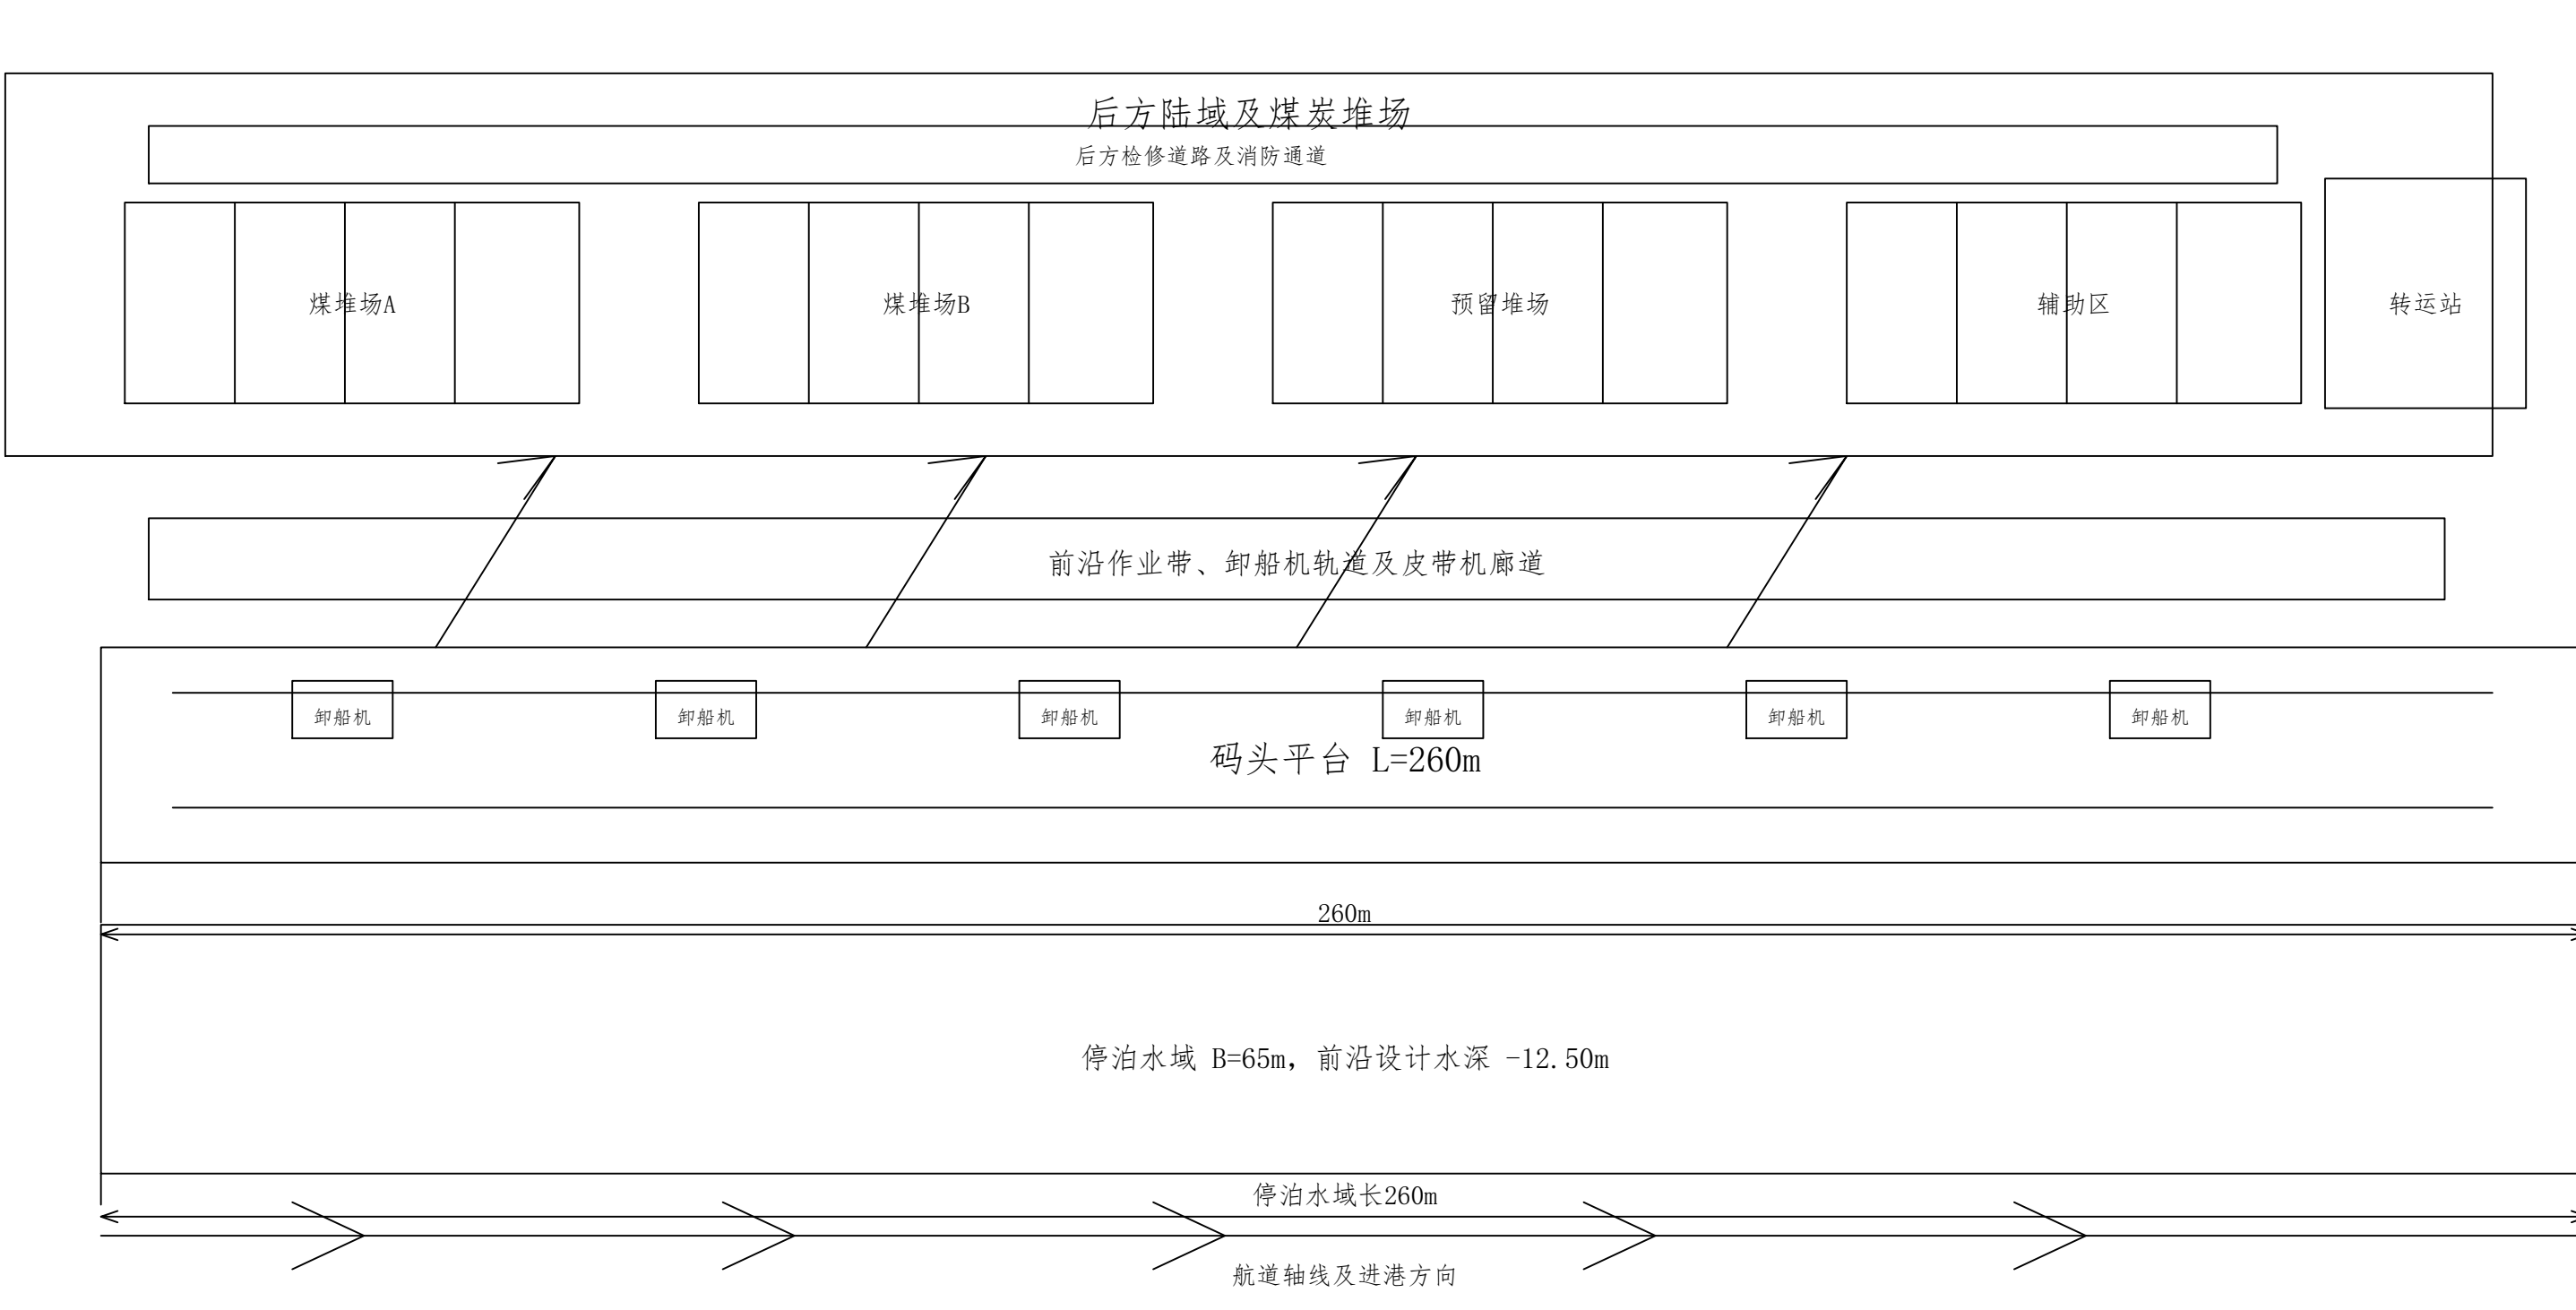


- 说明:
1. 本图按5万吨级散货船靠泊条件布置。
 2. 码头前沿布置卸船机轨道，后方设置皮带机廊道、转运站及堆场。
 3. 水域包括停泊水域、回旋水域和进出港航道。
- 图例
- 堆场及生产辅助区
 - 航道/轨道中心线
 - 码头平台及泊位

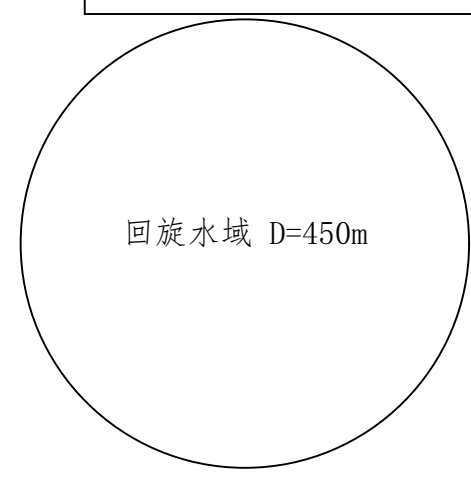

煤码头总平面布置图

汕尾电厂配套煤码头工程初步设计			
图名	煤码头总平面布置图		
比例	1:1000	图号	1/6
设计	潘欣	日期	2026. 06
指导教师	孙克俐	2022级港口二班 3022001703	