



沉箱平面布置

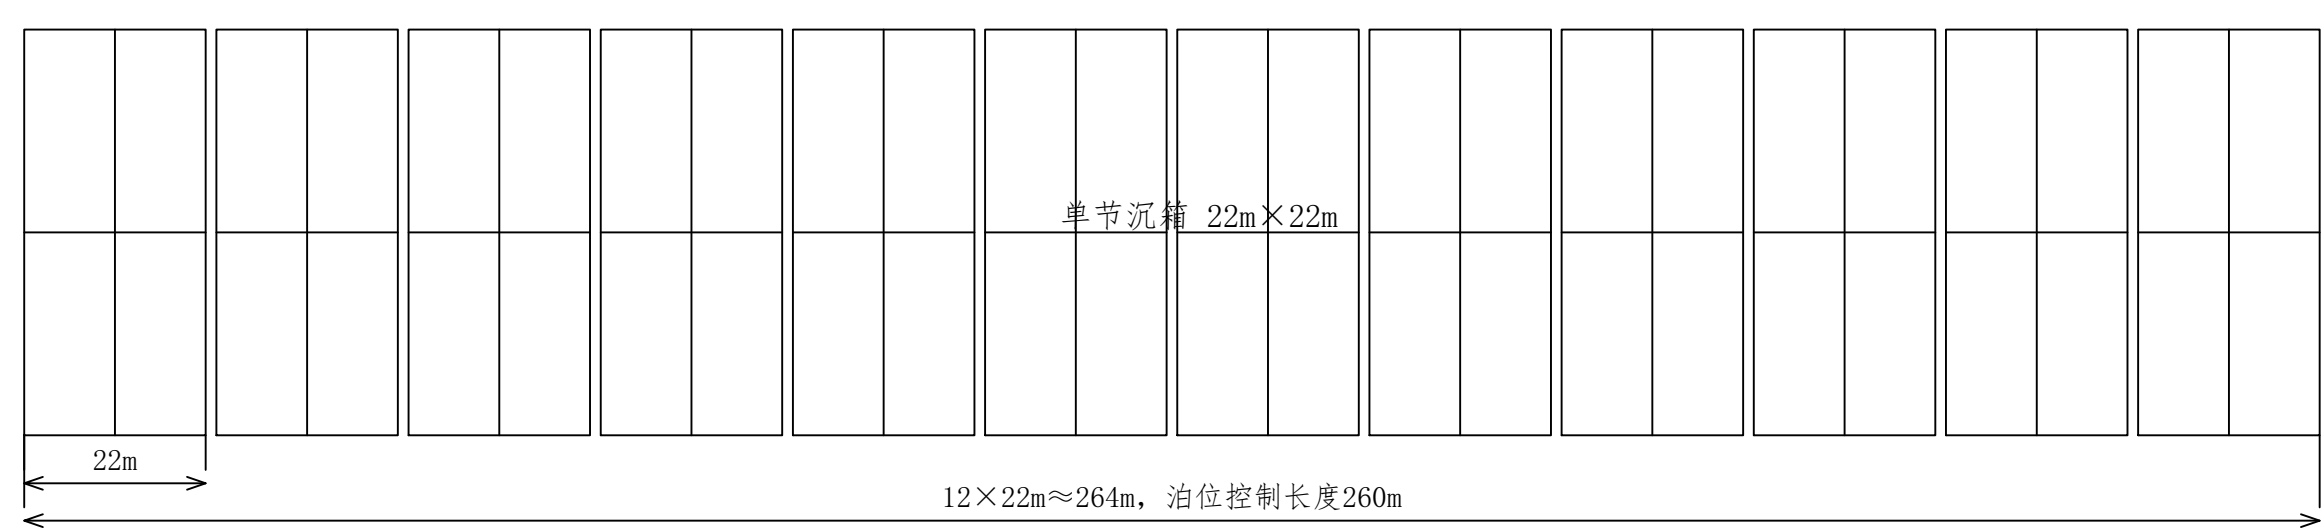

沉箱立面

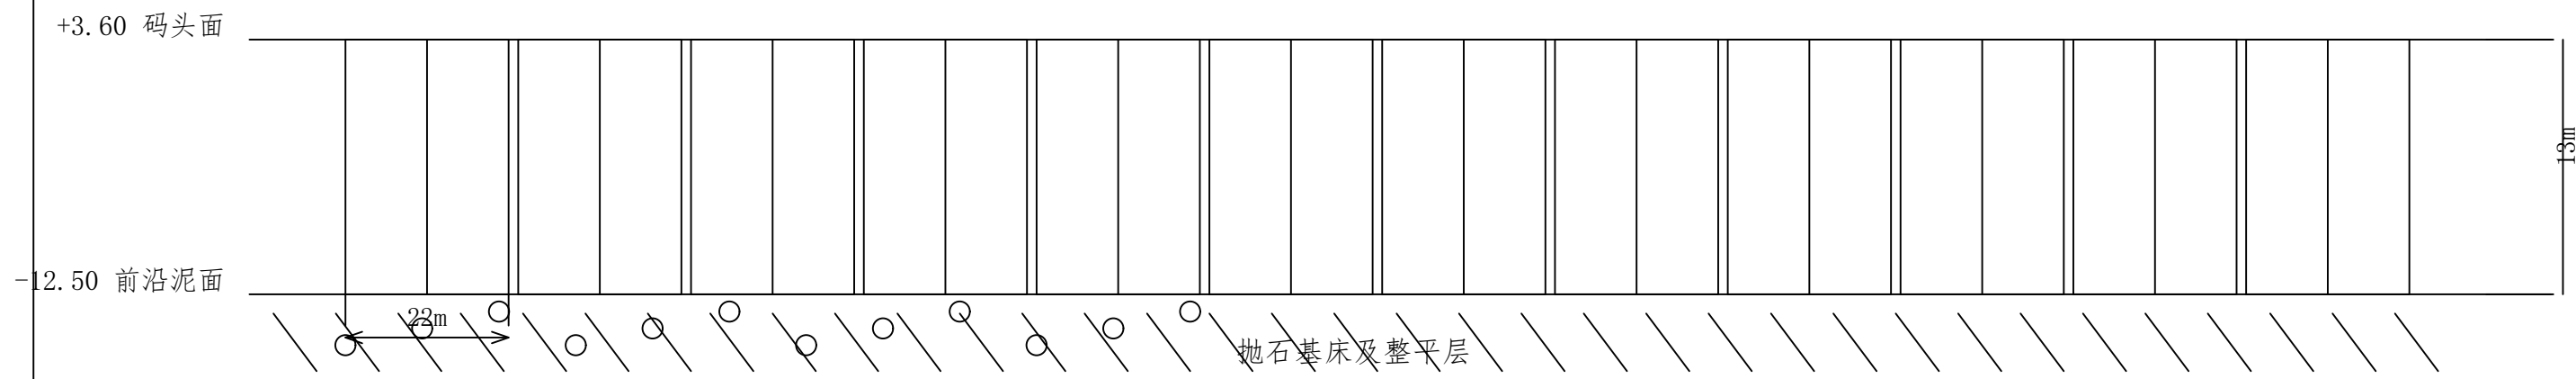

重力式沉箱方案平面、立面图

汕尾电厂配套煤码头工程初步设计			
图名	重力式沉箱方案平面、立面图		
比例	1:200	图号	4/6
设计	潘欣	日期	2026. 06
指导教师	孙克俐	2022级港口二班	3022001703