


纵梁、横梁及靠船构件断面图（单位：mm）

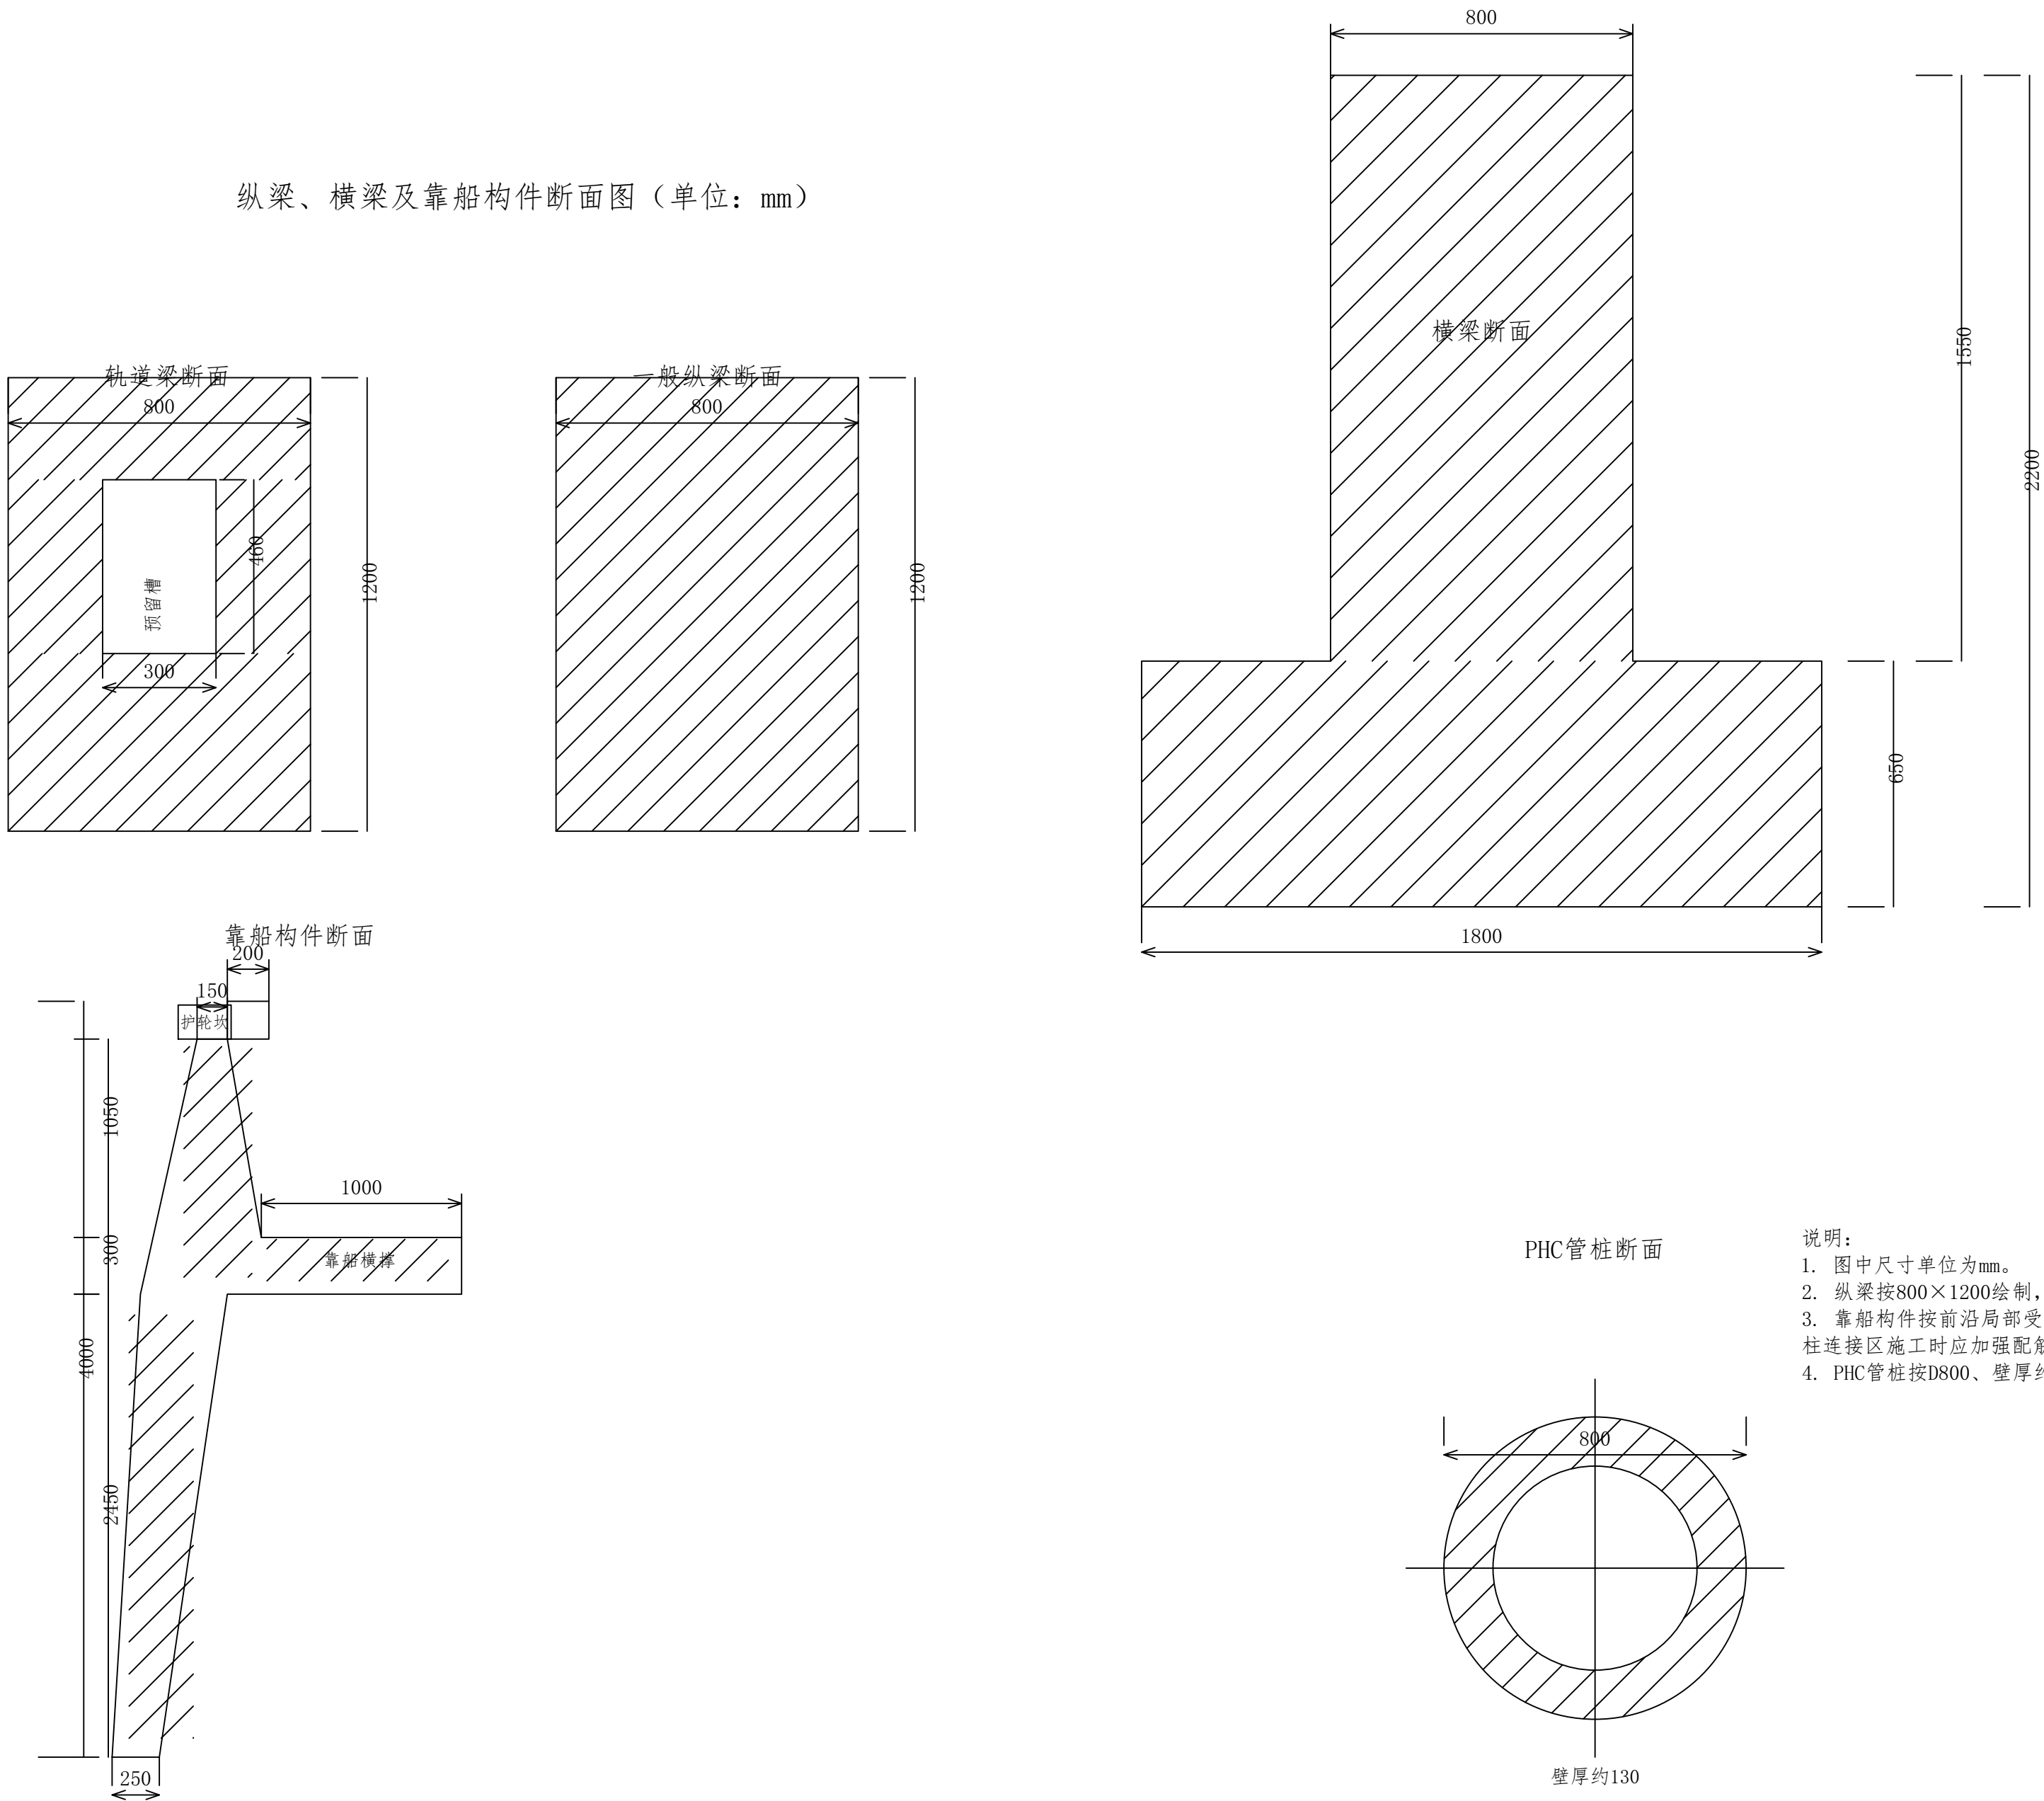

说明：
1. 图中尺寸单位为mm。
2. 纵梁按800×1200绘制，横梁按1800×2200控制。
3. 靠船构件按前沿局部受力构件绘制，护舷和系船柱连接区施工时应加强配筋。
4. PHC管桩按D800、壁厚约130绘制。

典型构件尺寸图

汕尾电厂配套煤码头工程初步设计			
图名	典型构件尺寸图		
比例	1:50	图号	6/6
设计	潘欣	日期	2026.06
指导教师	孙克俐	2022级港口二班	3022001703