



平面图

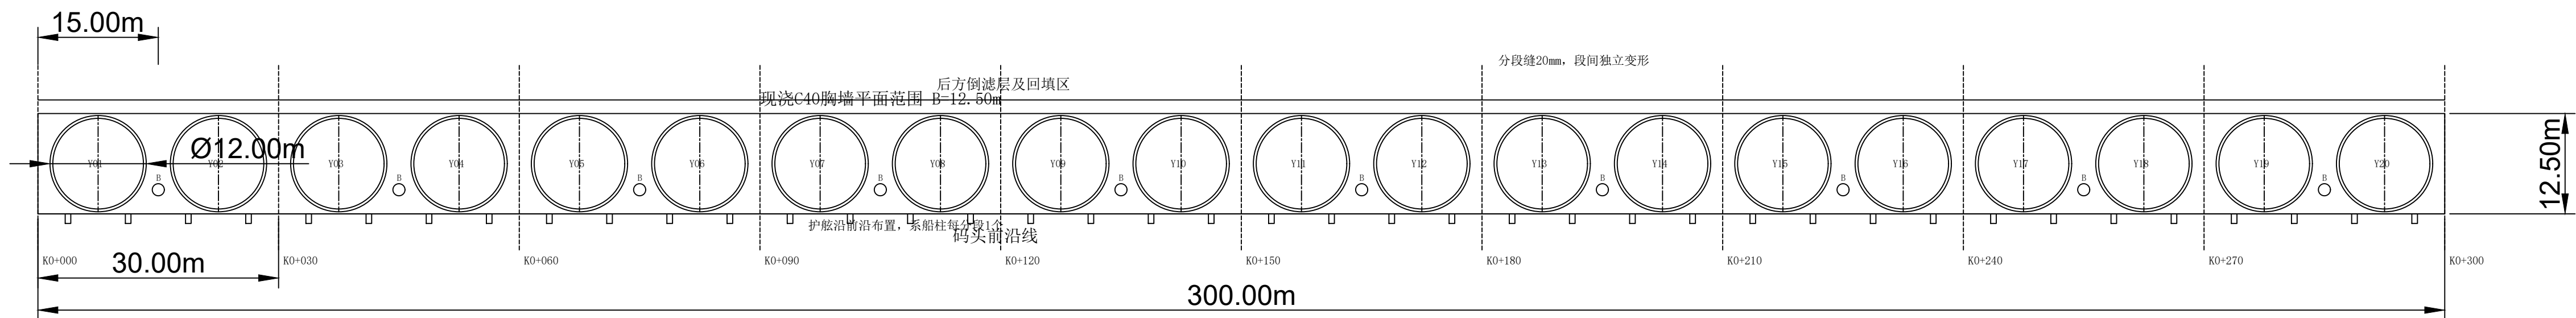

立面图

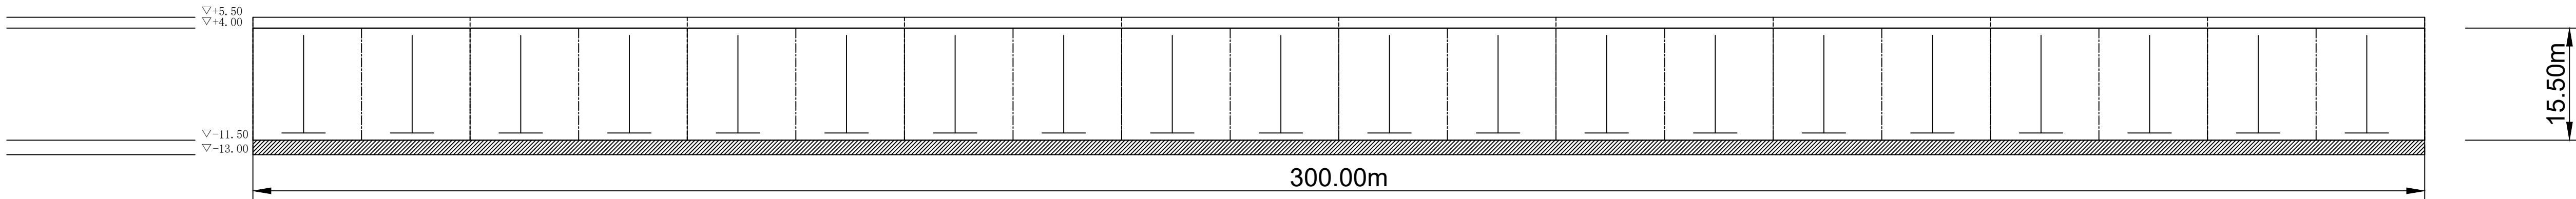

项目	设计值	说明
码头长度	300m	10个分段
大圆筒	20个	2个/分段
圆筒外径	12.0m	中心距15.0m
壁厚/高度	0.35m/15.5m	C45预制
附属设施	护舷2组/段, 系船柱1个/段	与胸墙锚固

大圆筒结构平面及立面图

大圆筒结构平面及立面图			比例 1:500
			图号 C-01
制图	褚喆	审核	褚喆
			港口一班