


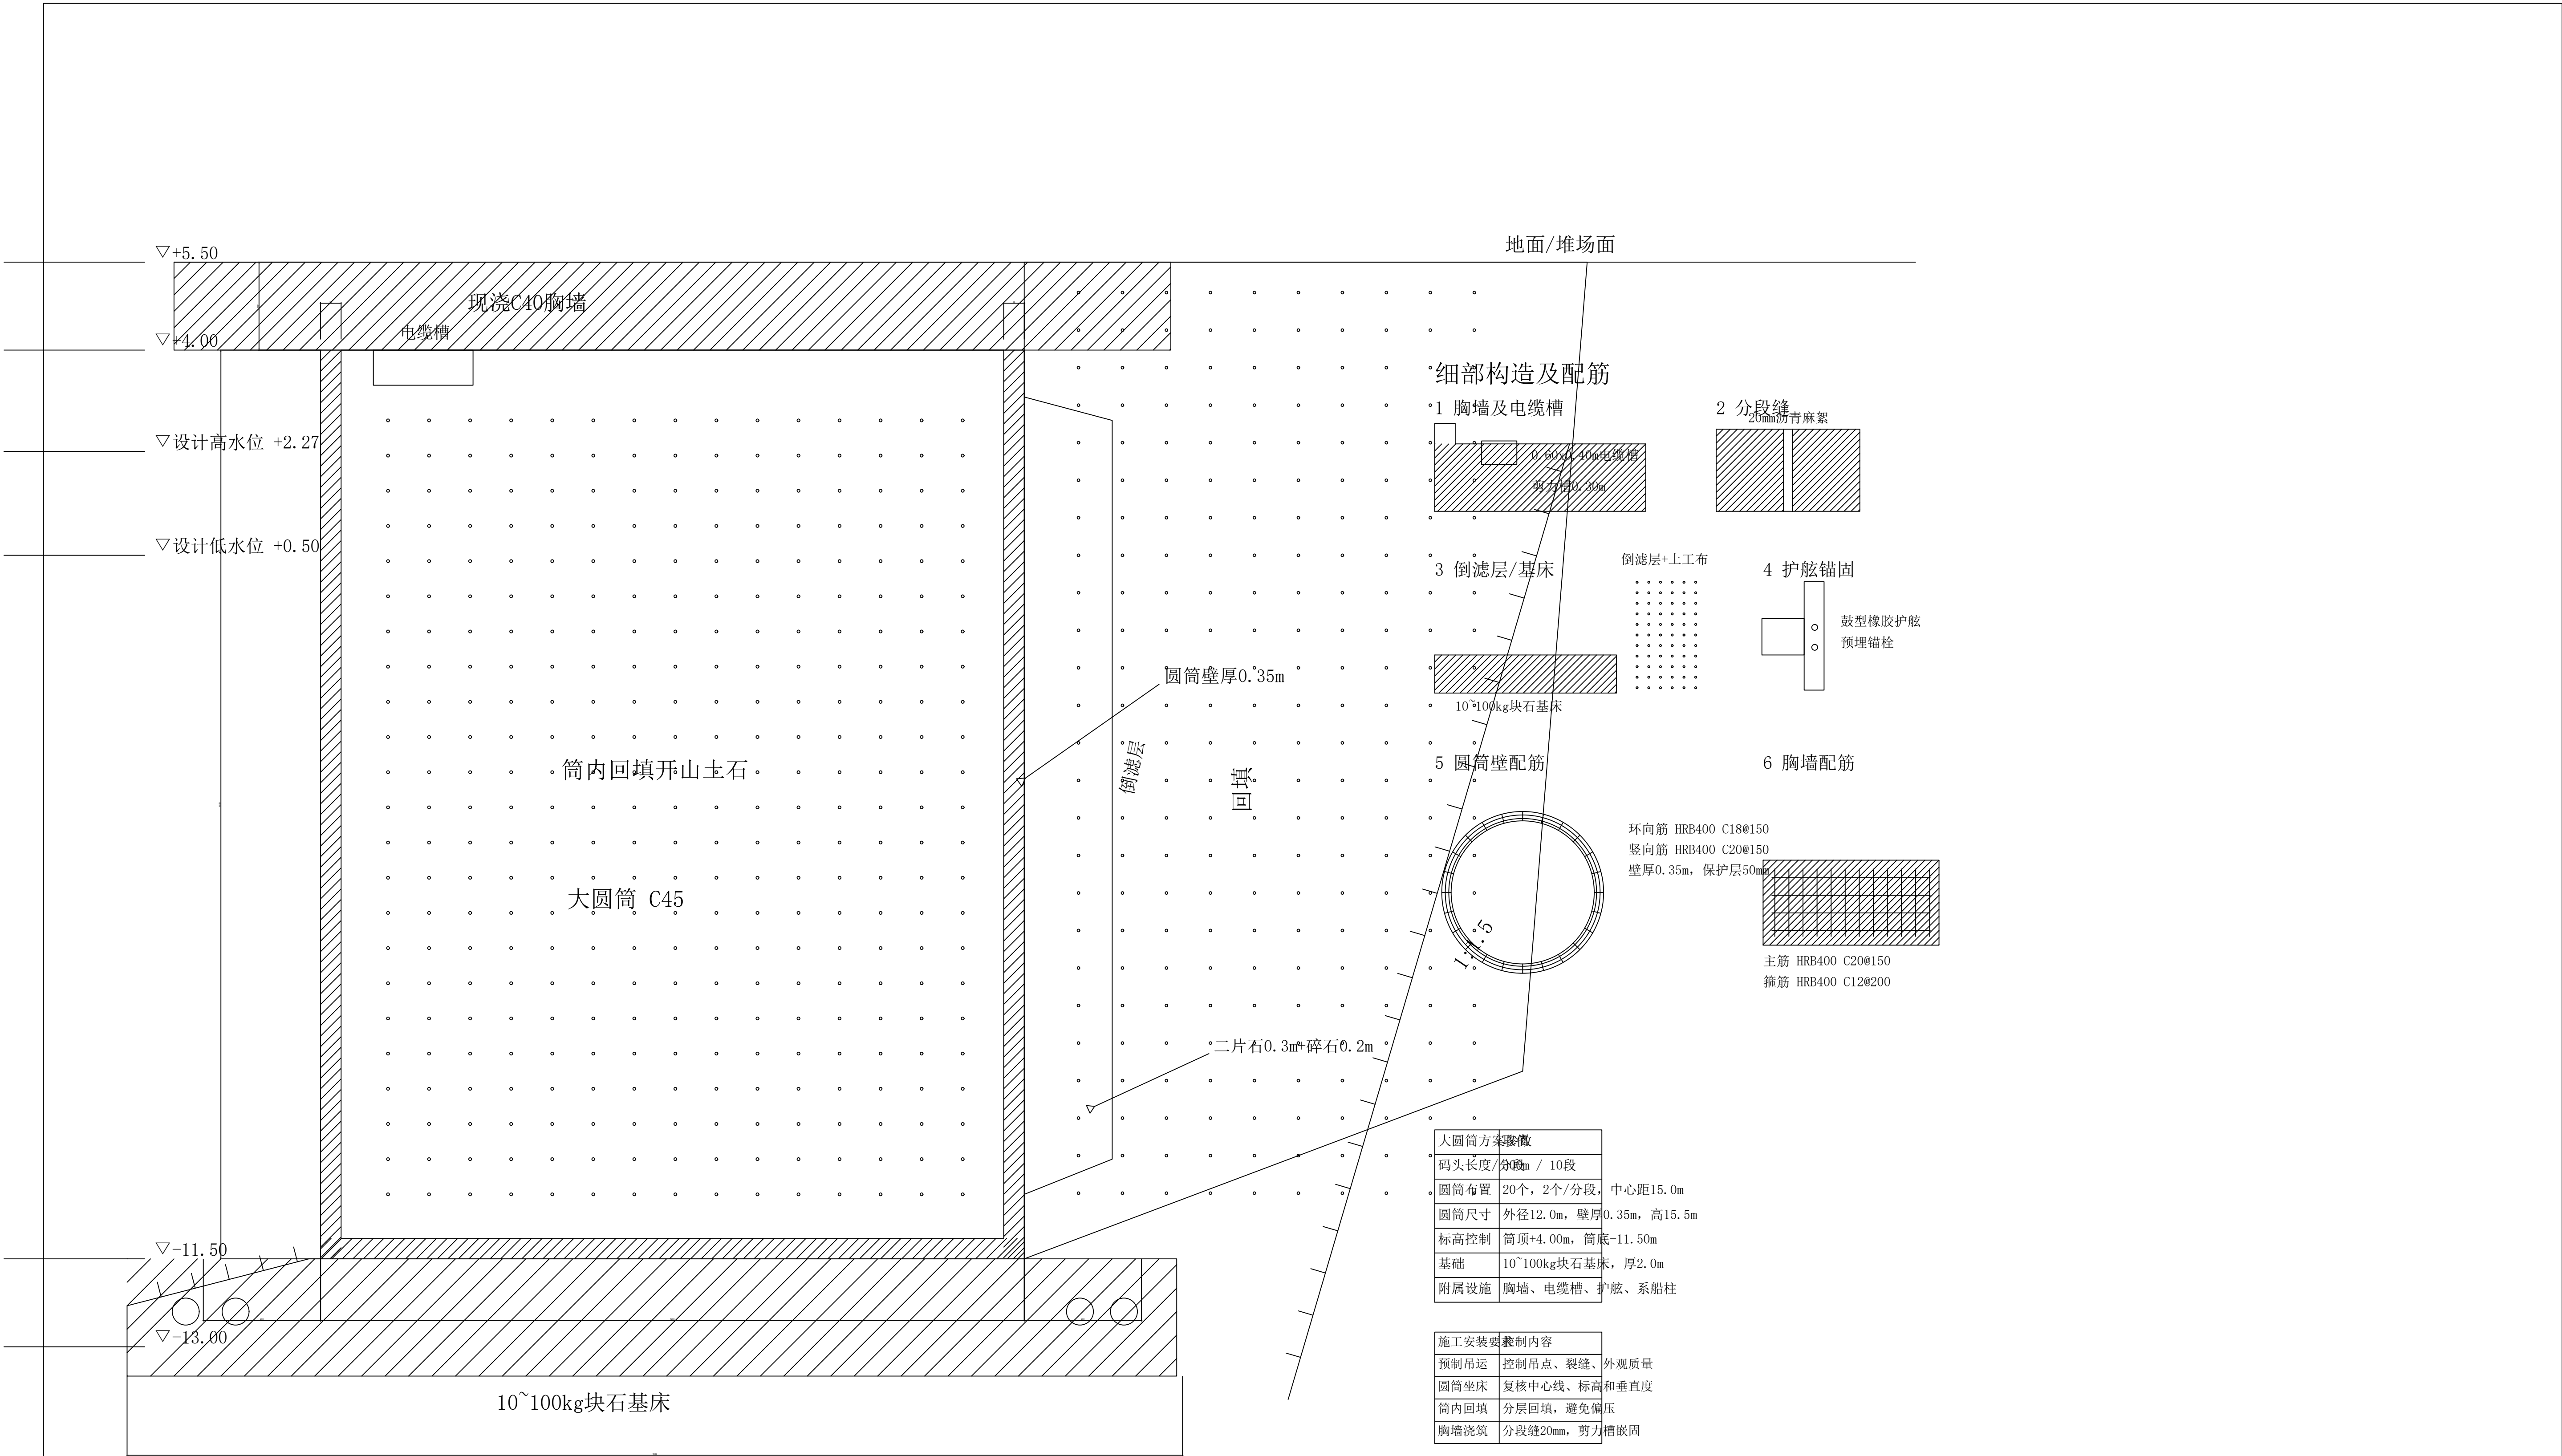

大圆筒结构断面、细部构造及代表配筋图

大圆筒结构断面、细部构造及代表配筋图			比例 1:100/1:50
制图 褚喆 审核 褚喆			图号 C-02
港口一班			