



平面图

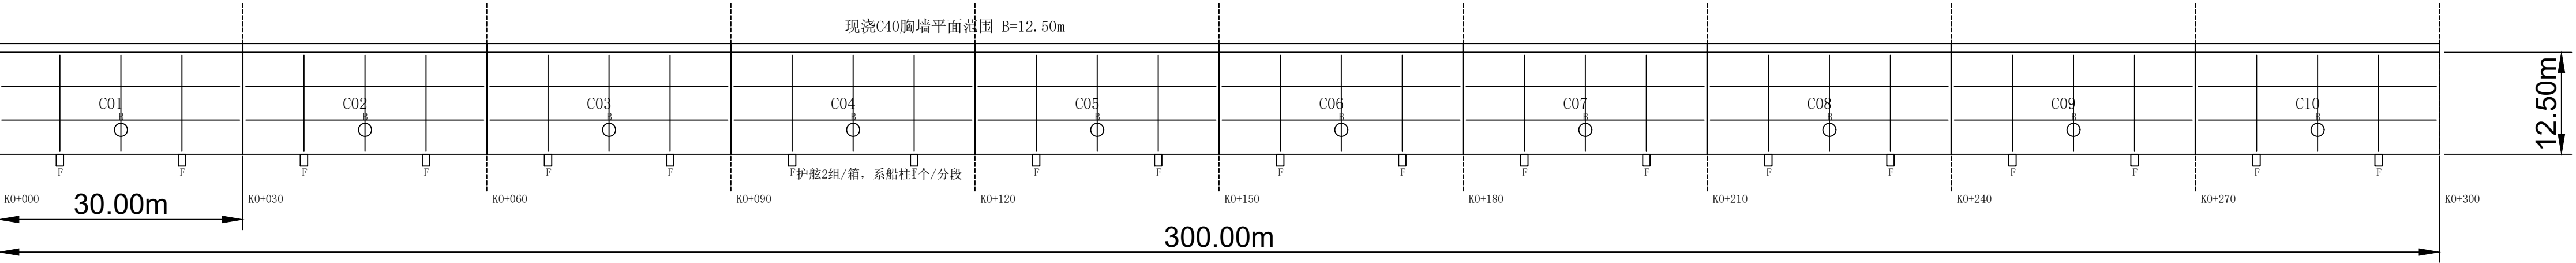

立面图

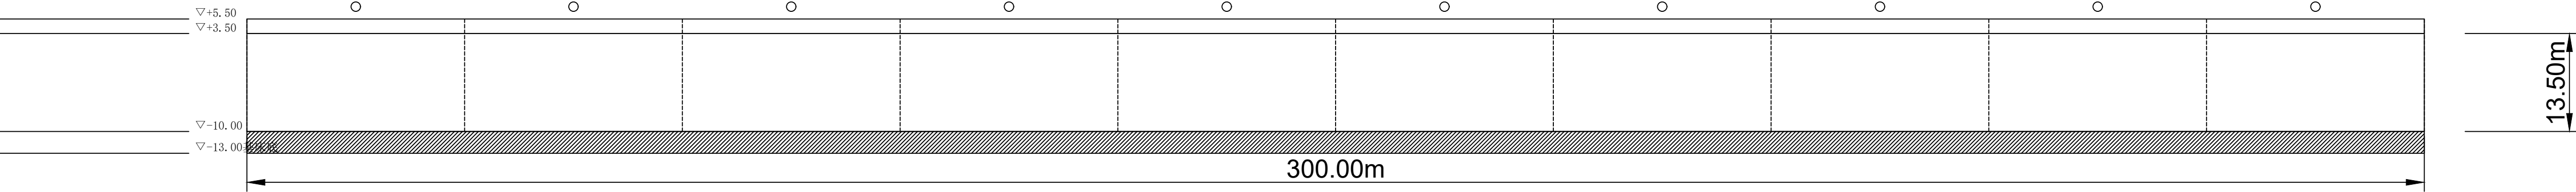

项目	设计值	说明
沉箱数量	10座	每30m一段
单座尺寸	29.95x12.50x13.50m	C45预制
舱格	3列x多格	外墙0.35m，内隔墙0.20m
胸墙	高2.0m，顶+5.50m	C40现浇，设剪力槽
附属设施	护舷20组，系船柱10个	沿前沿均布

注：本图为沉箱方案结构立面布置，断面、节点与配筋详见S-02。

沉箱结构平面及立面图

沉箱结构平面及立面图				比例 1:500
				图号 S-01
制图	褚喆	审核	褚喆	港口一班