



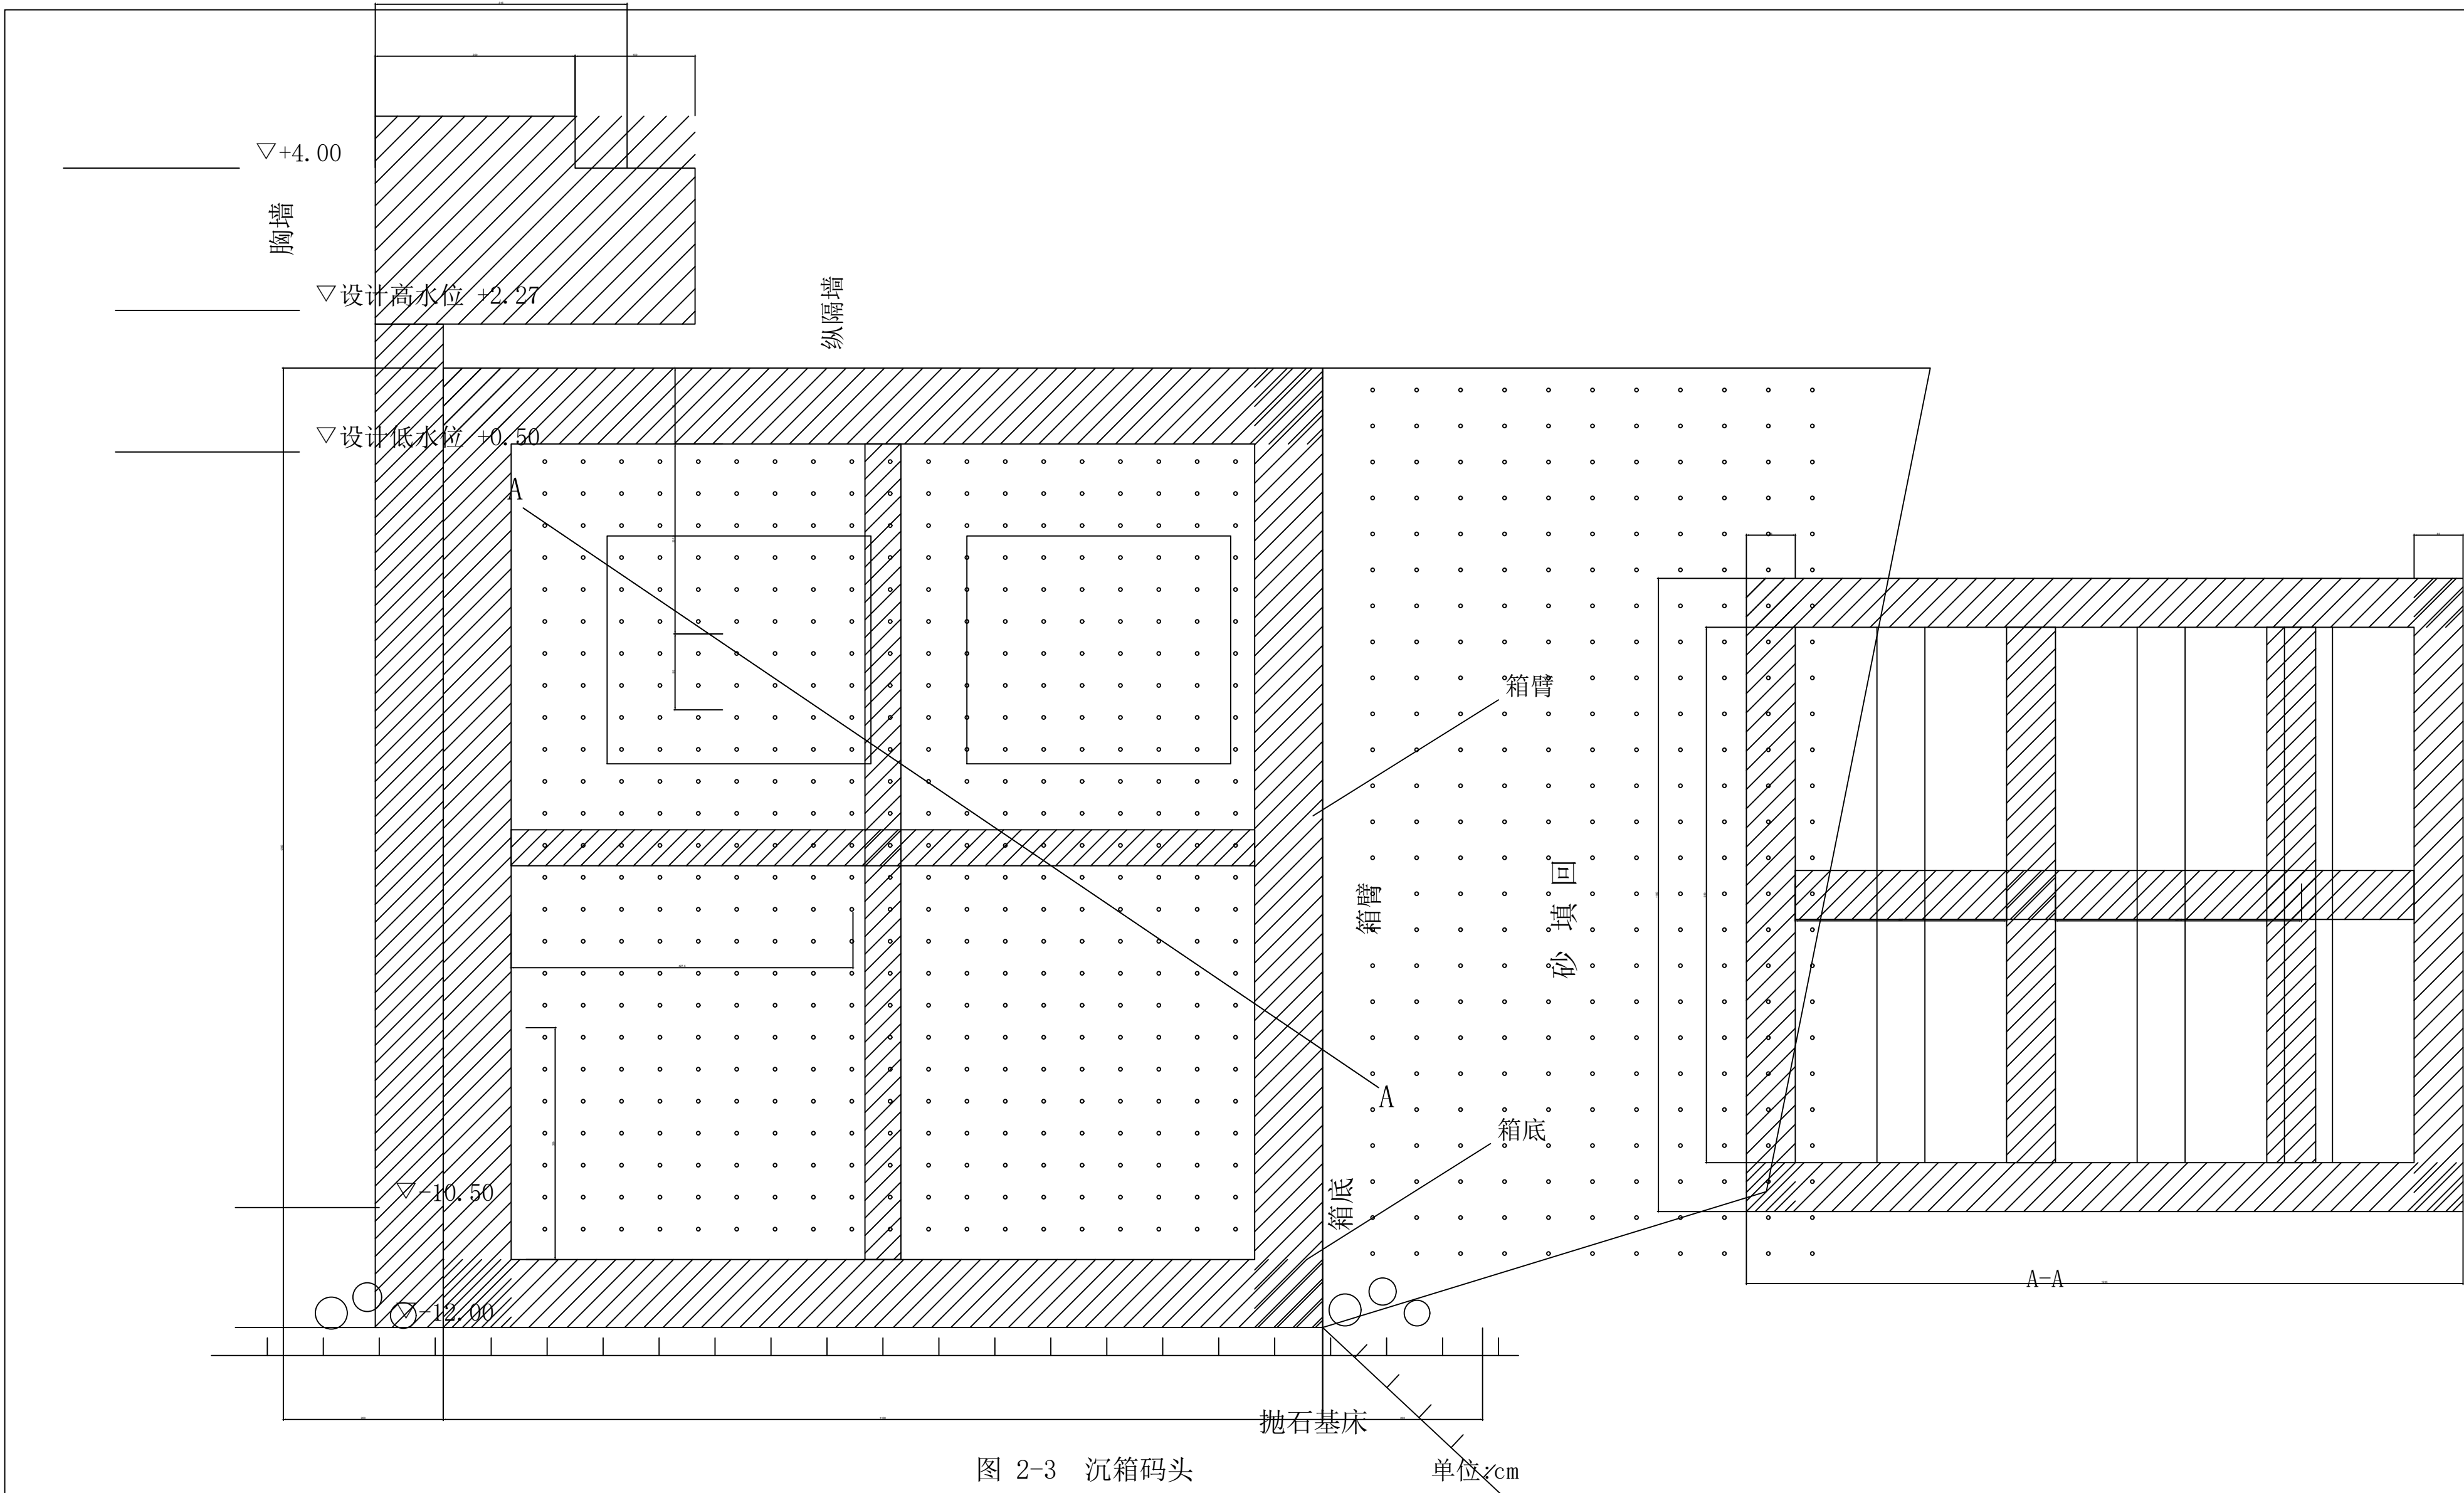


图 2-3 沉箱码头

细部构造

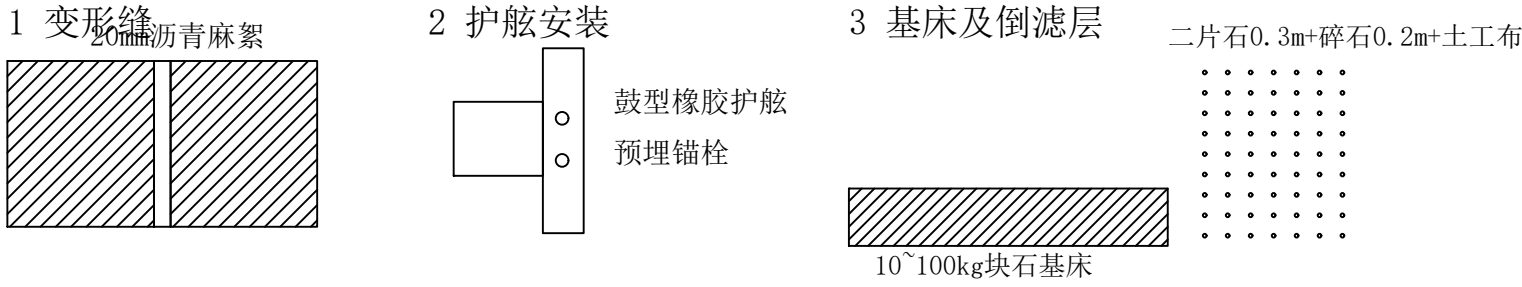

代表构件配筋

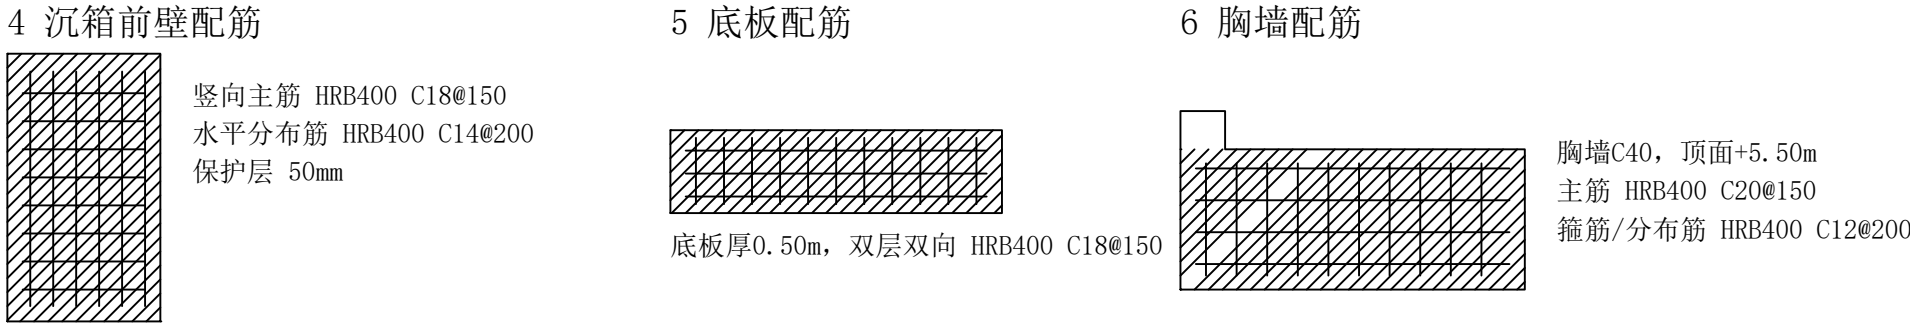

说明：本图按原沉箱示意图复刻断面，并将细部构造和代表构件配筋合并在同一张图纸内。

沉箱方案参数	取值
码头长度/分段	300m / 10段
单座沉箱	29.95m x 12.50m x 13.50m
结构材料	沉箱C45，胸墙C40
墙厚	外墙0.35m，内隔墙0.20m
附属设施	1500kN系船柱1个/段，护舷2组/箱

施工顺序	控制要点
1 基槽开挖	开挖至持力层并整平
2 基床抛石	分层抛填、夯实、整平
3 沉箱安装	定位、压载、坐床复测
4 回填/倒滤	分层回填，接缝处加厚倒滤
5 胸墙及面层	现浇、养护、安装附属设施

沉箱结构断面、细部构造及代表配筋图

			比例	1:100/1:50
沉箱结构断面、细部构造及代表配筋图			图号	S-02
制图	褚喆	审核	褚喆	港口一班