



沉箱平面布置

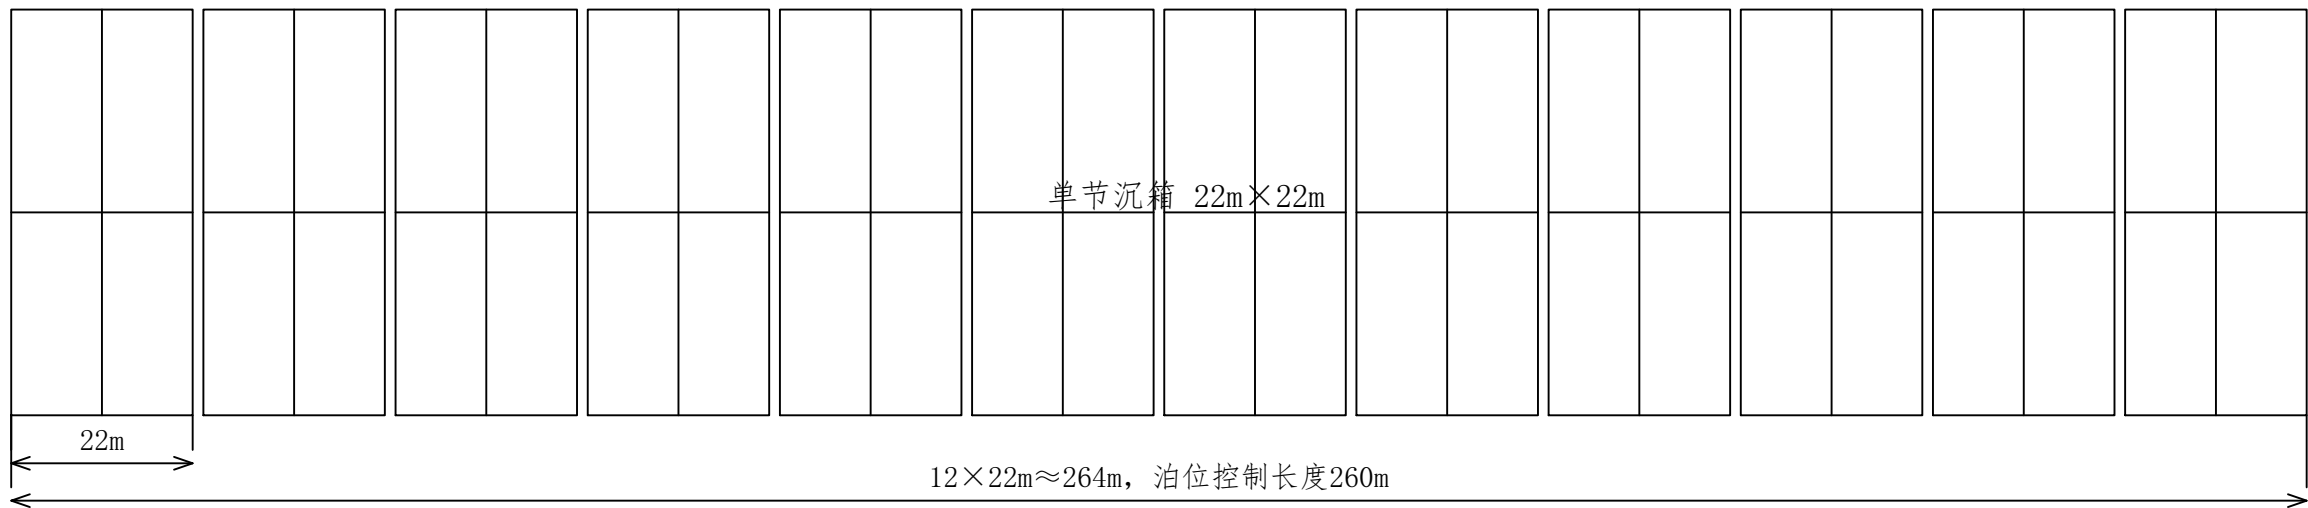

沉箱立面

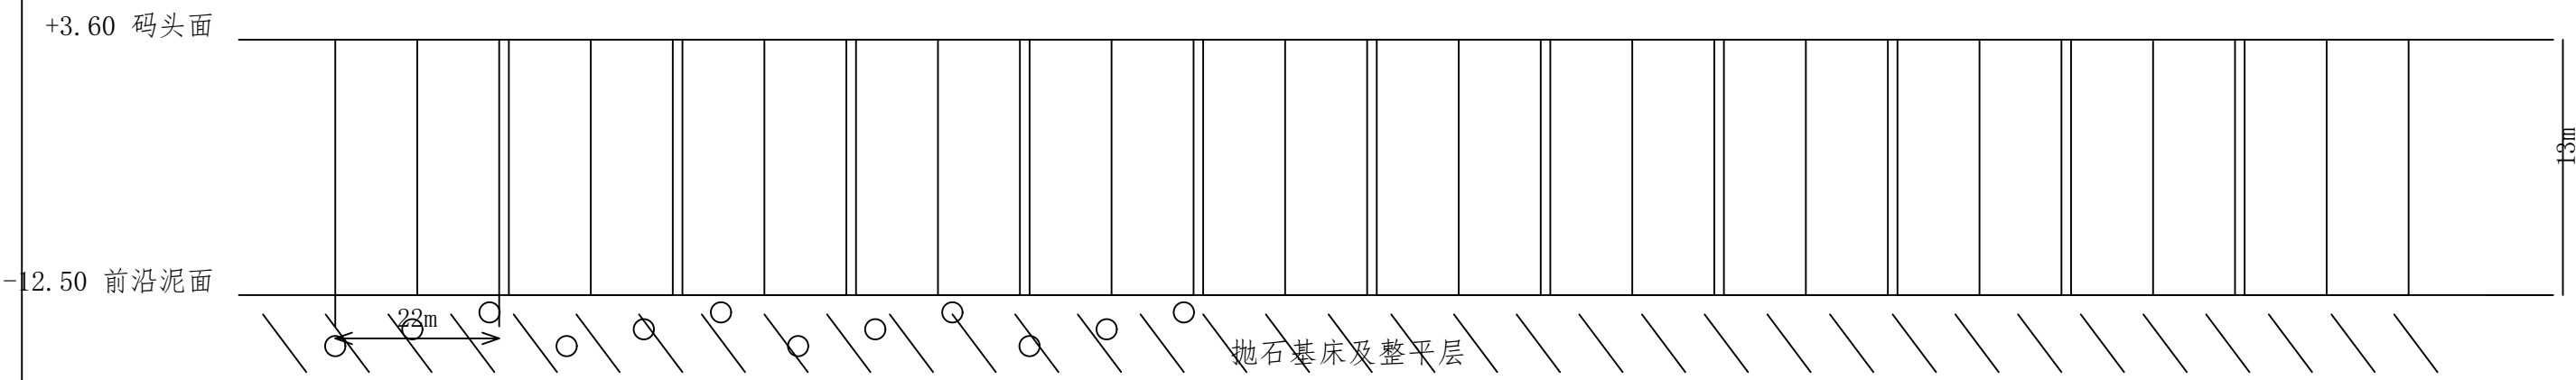

重力式沉箱方案平面、立面图

汕尾电厂配套煤码头工程初步设计		
图名	重力式沉箱方案平面、立面图	
比例	1:200	图号 4/6
设计	潘欣	日期 2026.06
指导教师	孙克俐	2022级港口二班 3022001703