

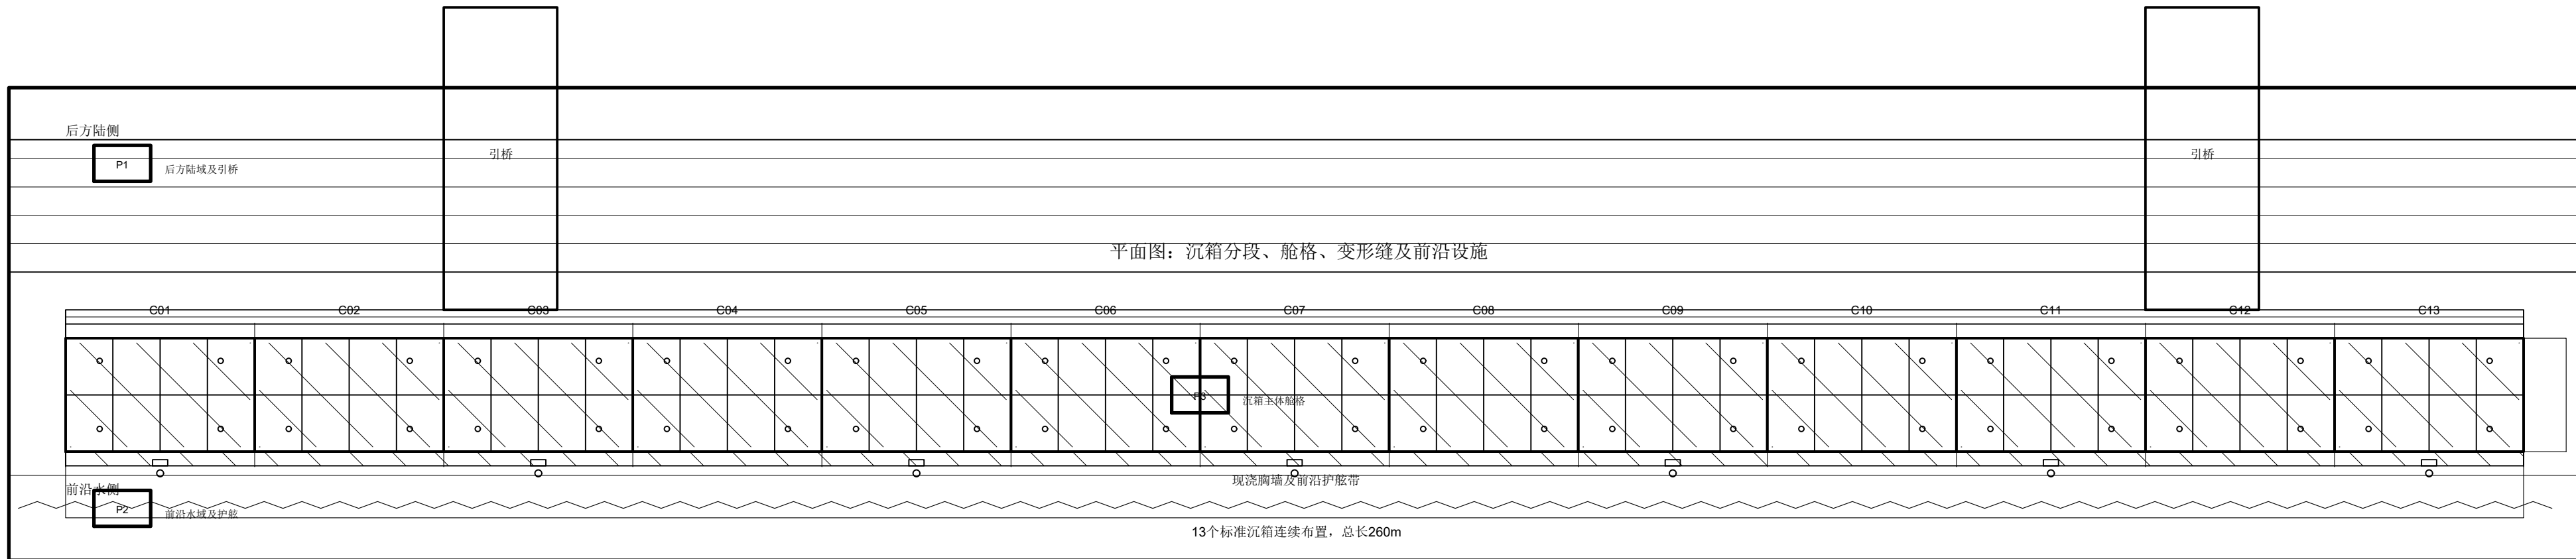
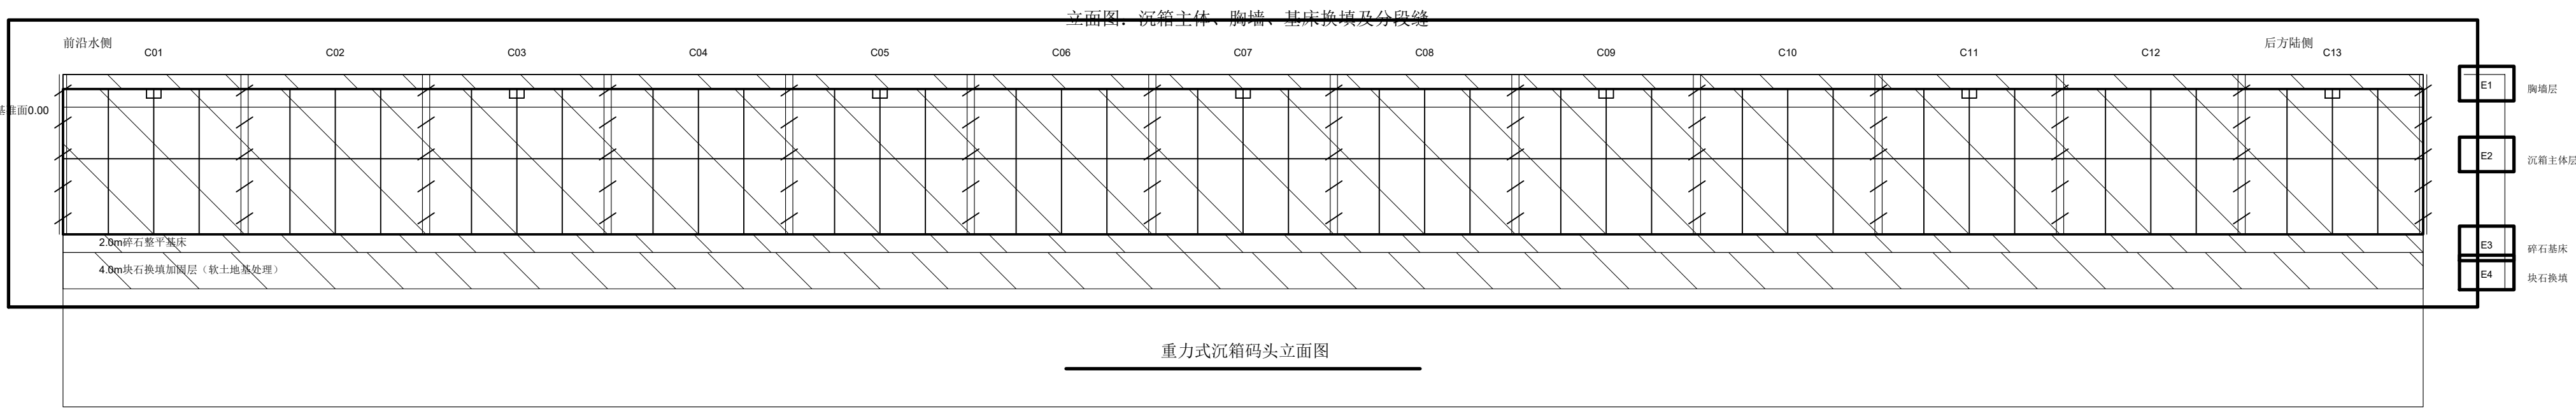


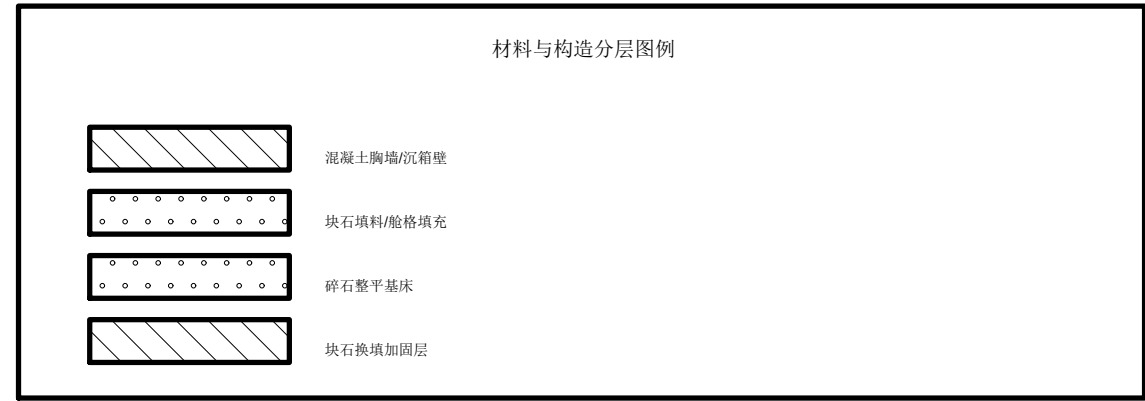

沉箱方案构件表		
项目	参数	表达重点
沉箱数量	13个	20m标准段连续布置
沉箱尺寸	20m x 12m x 14m	平面舱格与立面高度
基础处理	4m块石换填+20m碎石基床	软土地基加固层计算
上部结构	现浇胸墙+前沿护趾带	靠泊与系缆受力
现浇	变形缝+止水带	沉箱分段构造

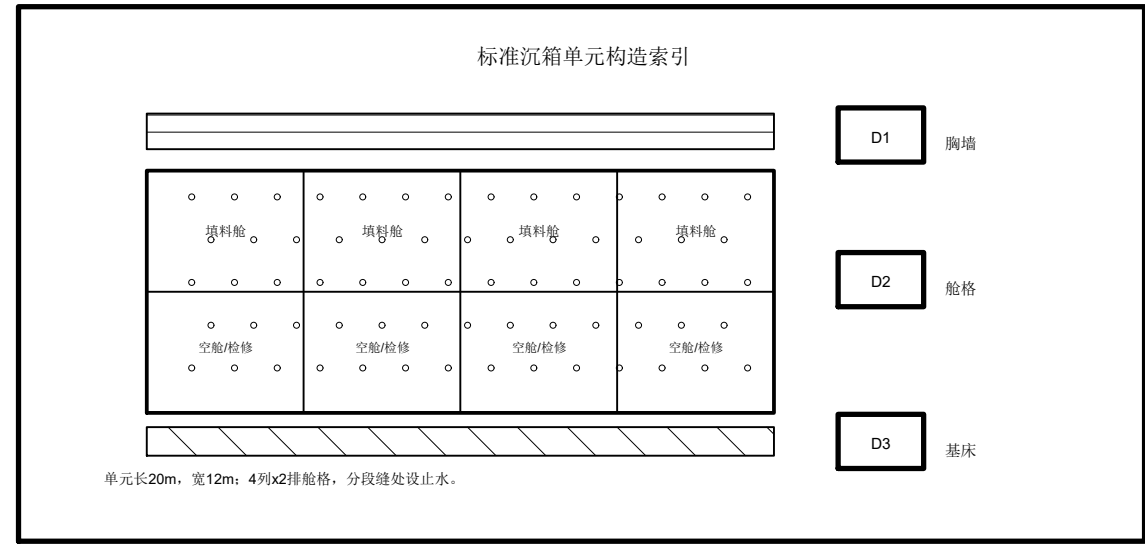

设计说明：

- 重力式方案按软土地基换填加固后进行沉箱抗滑、抗倾、基床承载和构造表达。
- 本工程天然软土地基不宜直接采用重力式结构，图中按换填加固后布置沉箱方案，用于完整计算和方案比选。
- 沉箱总长按13个20m标准箱布置，与总平面260m泊位长度一致。
- 本图作为两方案结构立面图之一，后续S-04给出横断面、稳定构造和代表配筋。

重力式沉箱结构平面、立面图

项目	汕尾电厂配套煤码头工程初步设计	编号	S-03
图名	重力式沉箱结构平面、立面图	比例	1:500
阶段	本科毕业设计-初步设计	日期	2026.05
设计	港口航道与海岸工程	指导	孙克刚
图幅	A1 横向	单位	mm/m
说明	按任务书及现行港工规范绘制	版本	五图重绘